



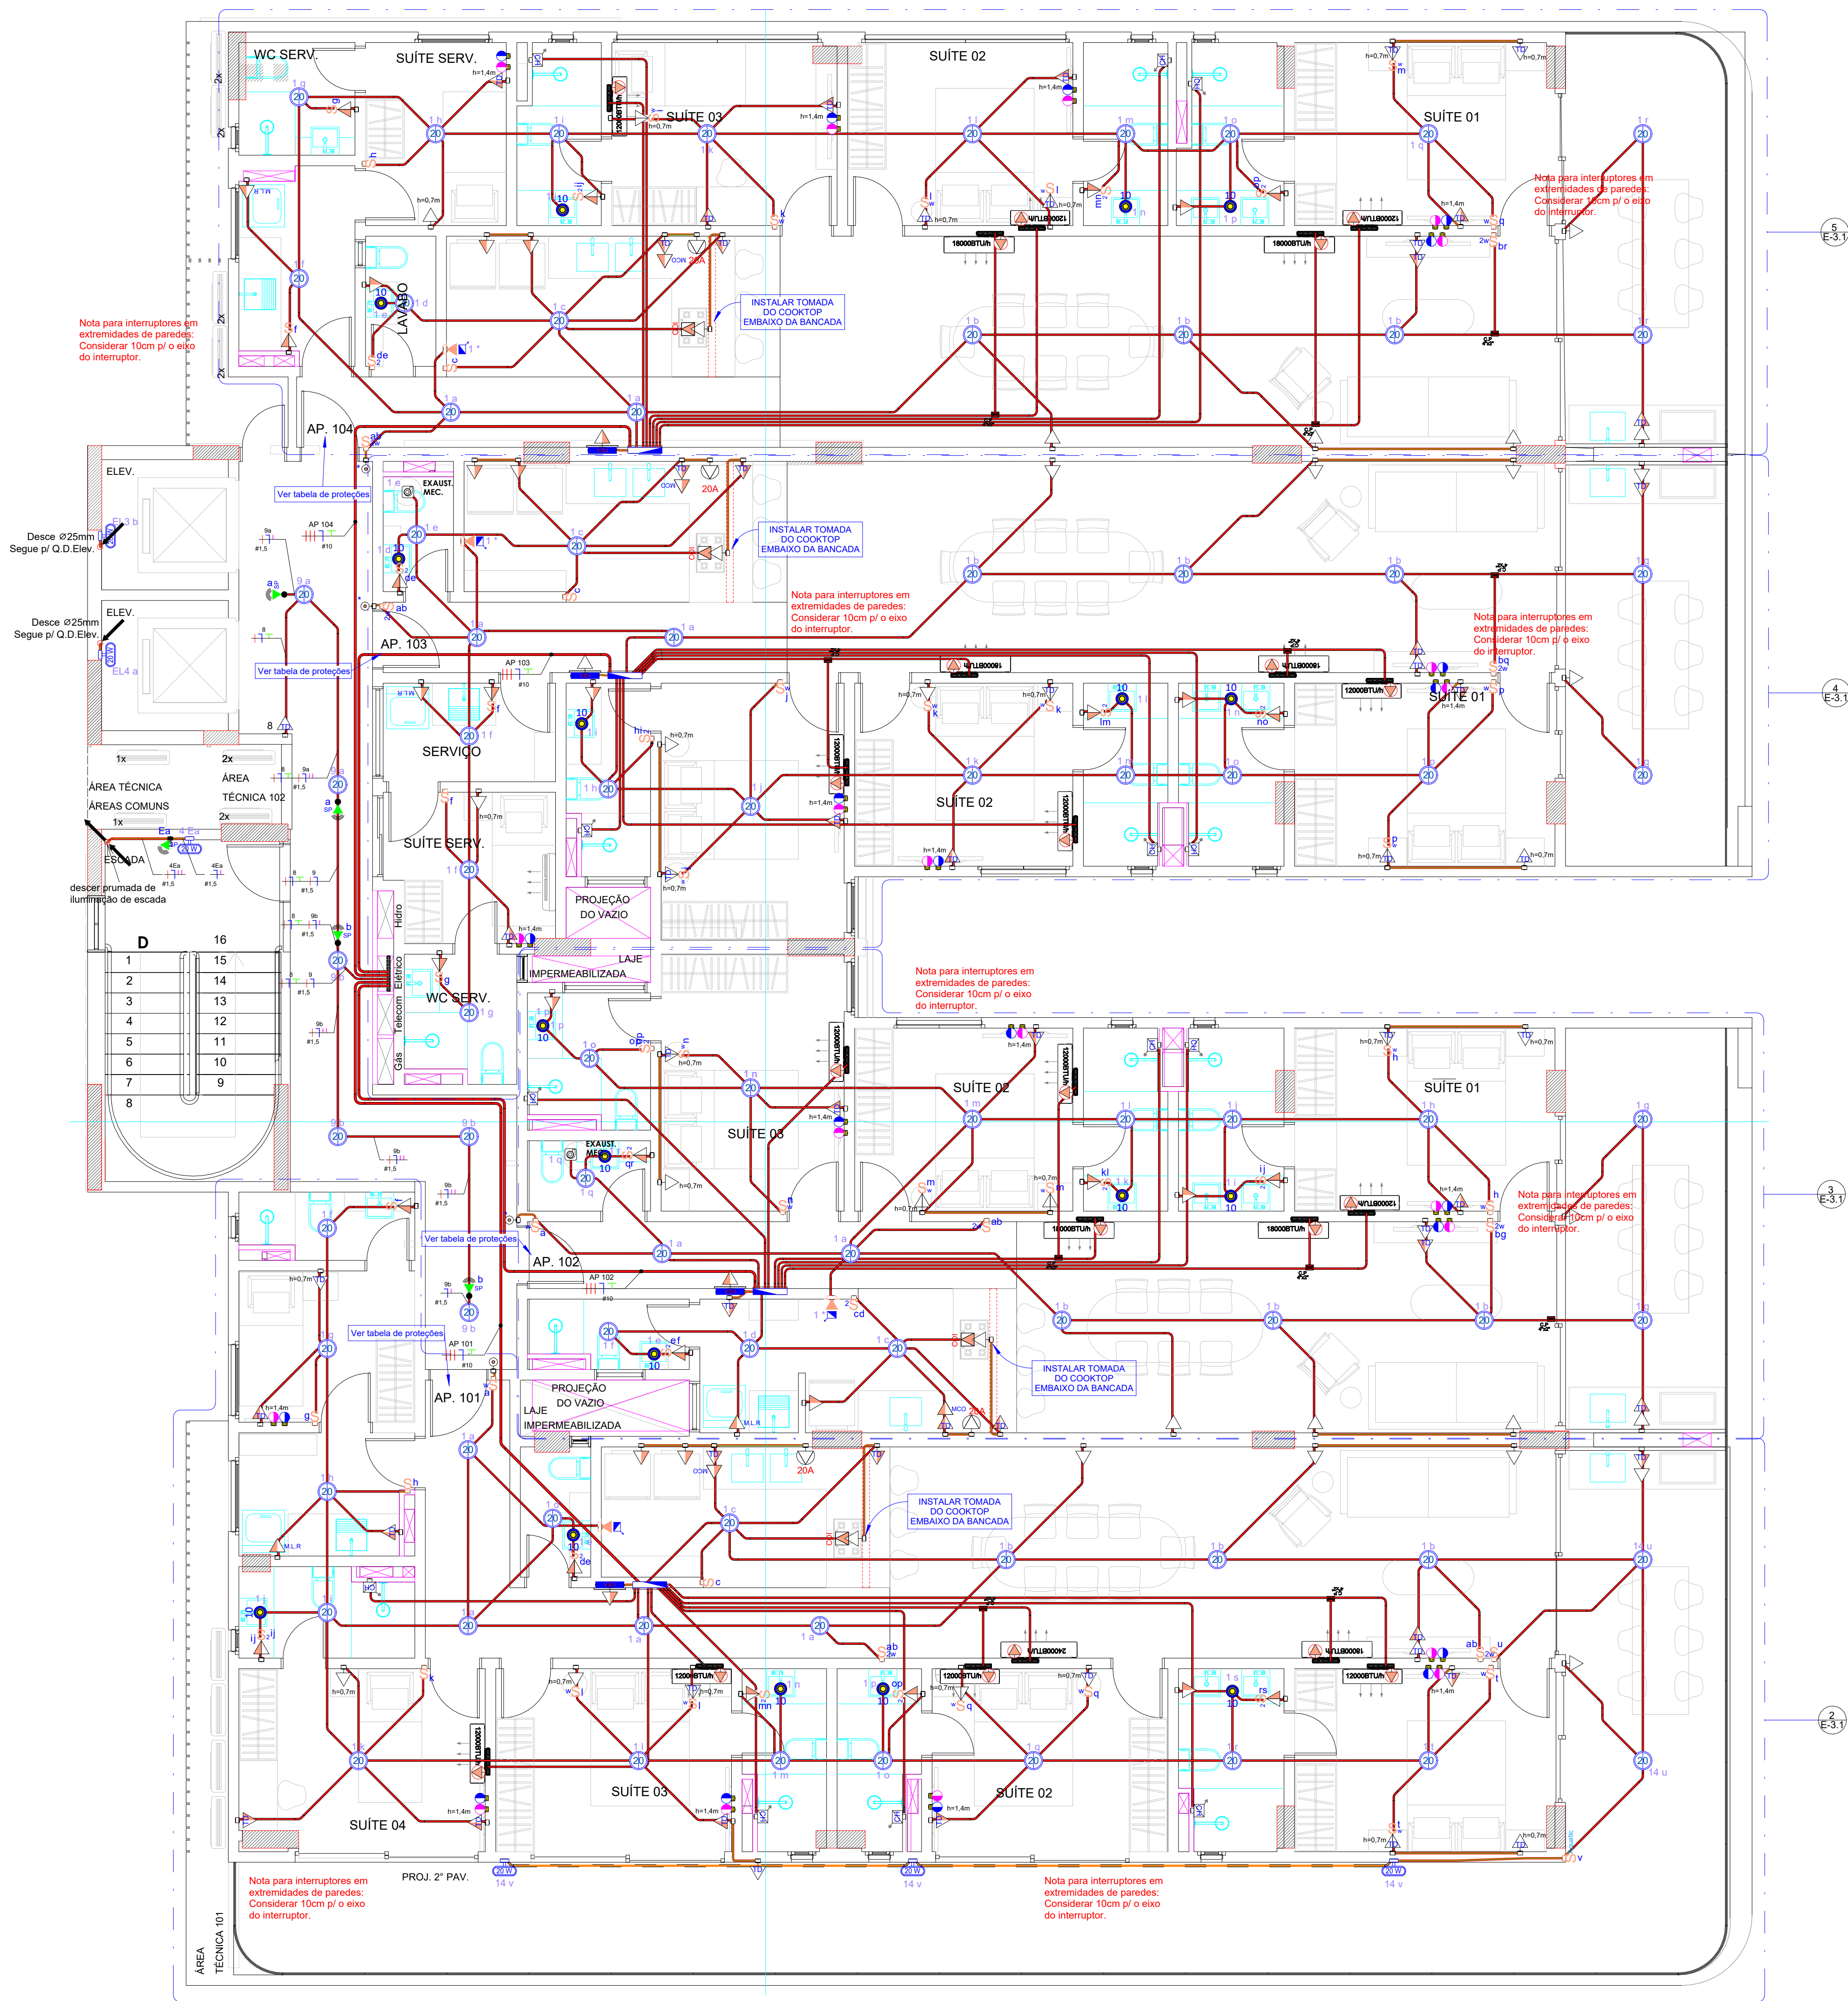


DETALHE FIXAÇÃO DO ELETRODUTO (ABRAÇADEIRA TIPO "D" DIRETA NA LAJE)

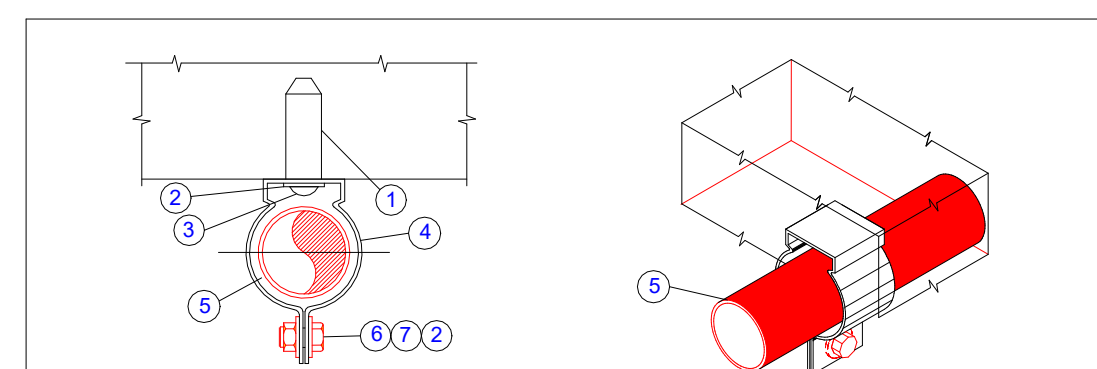


VALORES PARA UM MÓDULO DE FIXAÇÃO			
ITEM	DESCRIÇÃO	UNID.	QUANT.
01	BUCHA DE EXPANSÃO - NYLON - Ø 10mm	pg	1
02	ARRUELA LISA - Ø 5/16"	pg	2
03	PARAFUSO ROSCA LIGEIRA, FENDA PHILIPS, 40x6mm	pg	1
04	ABRAÇADEIRA "D" (1/2" - 3/4" - 1")	pg	1
05	ELETRODUTO - Ø 1/2", 3/4", 1"	m	Variável
06	PARAFUSO C/ CABEÇA SEXTAVADA - Ø 1/4" x 3/4"	pg	1
07	PORCA SEXTAVADA 3/16"	pg	1


DET. DE ENCAMISAMENTO (P/ PASSAGEM DE ELETRODUTO EM VIGA)

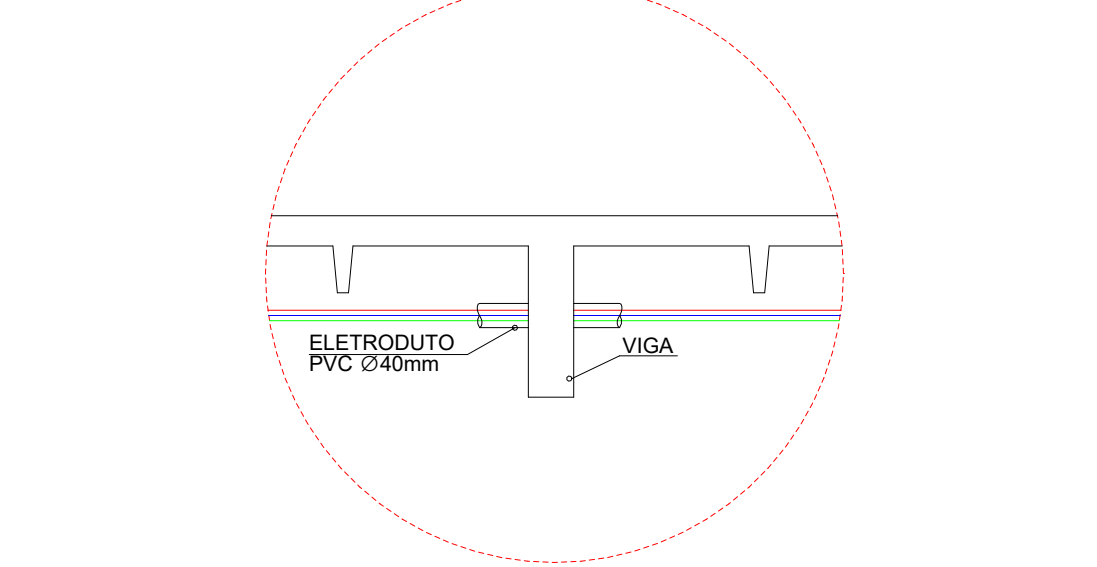

ELETRODUTO EMBUTIDO EM VIGA (VISTA EM CORTE)

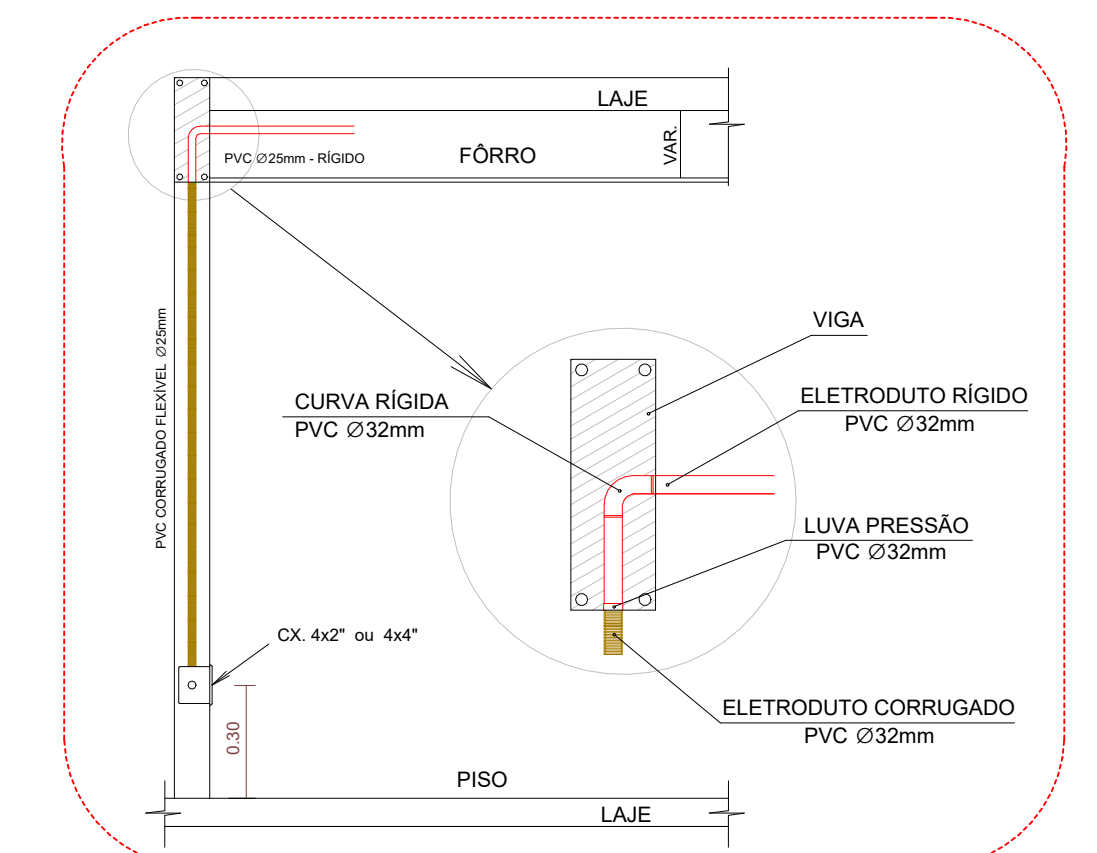

DESVIO DE ELETRODUTOS DA ESTRUTURA

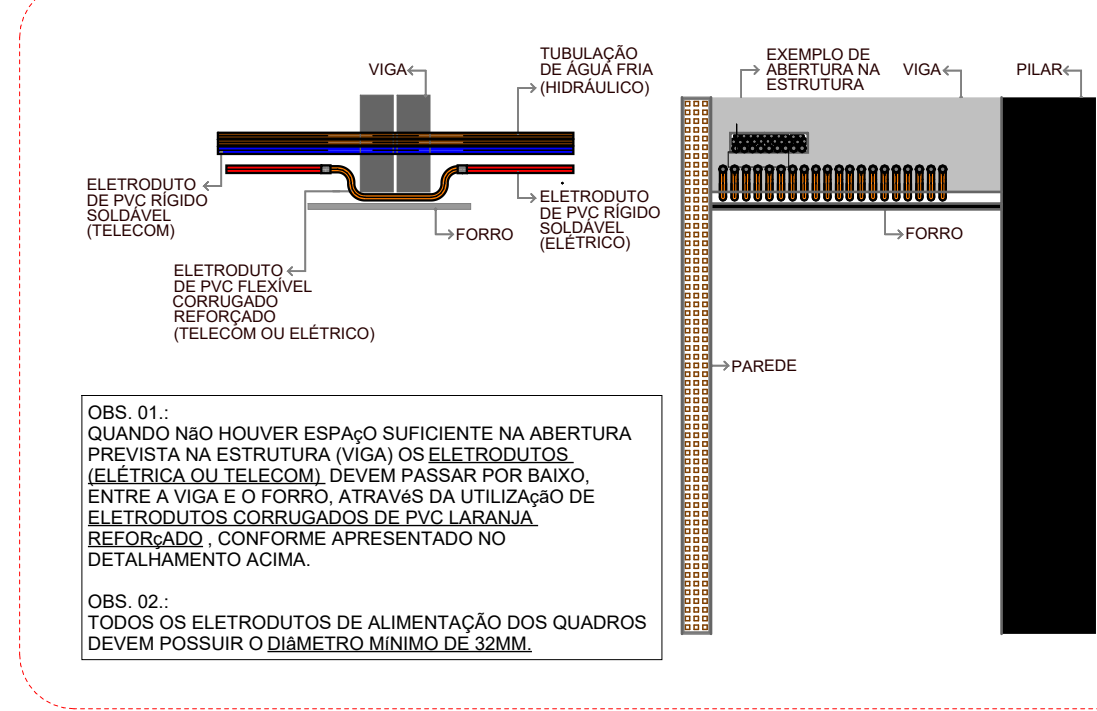

MGA MAKAI - QUADRO DE PROTEÇÕES		
NÚMERO DAS UNIDADES	TIPO DE LAYOUT	TIPO DE QUADRO
001	TIPO A	TIPO 1
101	TIPO B (COM VARANDA EM L)	TIPO 2
201, 301, 401, 501, 601, 701	TIPO B	TIPO 2
102, 202, 302, 402, 502, 602, 702	TIPO C	
103, 203, 303, 403, 503, 603, 703	TIPO D	TIPO 3
104, 204, 304, 404, 504, 604, 704	TIPO E	
801	TIPO F	TIPO 4

LEGENDA	
	RODA-TETO A SER EXECUTADO PARA VIABILIZAR AS INSTALAÇÕES
	ENGROSSO A SER EXECUTADO PARA VIABILIZAR AS INSTALAÇÕES
	PONTO PARA CHUVEIRO 32A, H=2,20M. UTILIZAR CONECTOR DE EMENDA TIPO BARRA 06 BORNES (VERTICAL E HORIZONTAL)
	EXAUSTOR MECÂNICO
	CAIXA 4x4" TIPO CONDULETE COM TAMPA CEGA
	CAIXA 4x4" TIPO PVC COM TAMPA CEGA
	CARREGADOR VEICULAR INDIVIDUAL - H=1,5m (Mono ou Trifásico)
	CARREGADOR VEICULAR COLETIVO - H=1,5m (Mono ou Trifásico)
	TOMADA PARA AR-CONDICIONADO H=2,50m
	PONTO DE TOMADA, SIMPLES E DUPLA, 10A + 1 MÓDULO USB
	PONTO DE TOMADA, 20A - (VERTICAL E HORIZONTAL) - VERIFICAR AS ALTURAS ABAXO
	TOMADA ALTA H=2,20m, 10A - (VERTICAL E HORIZONTAL)
	TOMADA MÉDIA H=1,20m, 10A - (VERTICAL E HORIZONTAL) - MODO GERAL TV
	TOMADA BAIXA H=0,30m, 10A - (VERTICAL E HORIZONTAL)
	TOMADA TRÍPLA, 10A - (VERTICAL E HORIZONTAL)
	TOMADA DUPLA, 10A - (VERTICAL E HORIZONTAL)
	PONTO DE FORÇA PARA MOTOR DE PORTÃO DE GARAGEM - 1/2 CV
	TOMADA DE TETO - EMBUTIDA NO FORRO OU LAJE, 10A (SIMPLES E DUPLA)
	TOMADA DE TETO - EMBUTIDA NO FORRO OU LAJE, 20A (SIMPLES E DUPLA)
	TOMADA DE PISO SIMPLES E DUPLA, 10A
	TOMADA ALTA COÍFA FOGÃO H=1,80m, 10A
	TOMADA P/ FORNO MICROONDAS (FANT) 20A, H=1,60m (VERTICAL E HORIZONTAL)
	TOMADA P/ FORNO ELÉTRICO (FANT) 20A, H=0,60m
	TOMADA P/ COZINHO (FANT) 20A, H=0,60m - COZINHO 2 E 4 BOCAS
	TOMADA MÁQUINA LAVAR ROUPA (FANT) 20A, H=1,20m
	PONTO PARA INTERFONE H=1,40m
	PONTO BAIXO PARA ANTENA COLETIVA H=0,30m
	PONTO MÉDIO PARA ANTENA COLETIVA H=1,50m
	PONTO ALTO PARA ANTENA COLETIVA H=1,80m
	TOMADA MÉDIA PARA TELEFONE H=1,20m
	TOMADA BAIXA PARA TELEFONE H=0,30m
	PONTO BAIXO PARA TV ASSINATURA H=0,30m
	PONTO MÉDIO PARA TV ASSINATURA H=1,50m
	PONTO ALTO PARA TV ASSINATURA H=1,80m
	INTERRUPTOR DE 1" SEÇÕES H=1,20m
	INTERRUPTOR SIMPLES 10A, H=1,20m
	INTERRUPTOR PARALELO, H=1,20m
	INTERRUPTOR INTERMEDIÁRIO, H=1,20m
	BOTONEIRA PARA CAMPAINHA, H=1,20m
	PONTO PARA CAMPAINHA H=2,10m
	LUMINÁRIA PLAFON CIRCULAR DE SOBREPOR P/ CIRCUITO DE ILUMINAÇÃO VIGA
	LUMINÁRIA PLAFON CIRCULAR DE SOBREPOR NO FORRO
	LUMINÁRIA PLAFON QUADRADA DE SOBREPOR NO FORRO
	SPOT LED QUADRADO EMBUTIDO NO FORRO
	SPOT LED REDONDO EMBUTIDO NO FORRO
	SPOT LED REDONDO (DUPLA) EMBUTIDO NO FORRO
	LUMINÁRIA FLUORESCENTE NA PAREDE 20W, H=1,8m
	PONTO DE REFLETOR NA PAREDE 20W, H=2,20m OU INDICADO
	PONTO DE ILUMINAÇÃO DE PAREDE - ARANDELA 20W, H=1,5m OU INDICADO
	TRILHO ELETRIFICADO - 10W POR SPOT
	LUMINÁRIA TIPO REFLETOR LED - 50W P/ FIXAÇÃO EM POSTE METÁLICO
	BALIZADOR DE PISO
	FITA DE LED NO TETO E PAREDE - (VER POTÊNCIA EM PLANTA BAIXA)
	FITA DE LED NO PISO - (VER POTÊNCIA EM PLANTA BAIXA)
	CAIXA OCTOGONAL OU 4x2" + FONTE (DRIVER) PARA FITA DE LED
	CAIXA SODRAMPAR, PARA UTILIZAÇÃO NA ILUMINAÇÃO DA PISCINA
	SENSORES DE PRESENÇA DE TETO
	SENSOR DE PRESENÇA DE PAREDE
	CONDUTORES NEUTRO, FASE, TERRA E RETORNO
	ELETRODUTO PVC RÍGIDO NO ENTREFORRO OU EMBUTIDO NA LAJE
	ELETRODUTO PVC CORRUGADO REFORÇADO EMBUTIDO NA PAREDE
	ELETRODUTO PVC RÍGIDO SOB LAJE DE PISO
	ELETRODUTO PVC RÍGIDO NO PISO PARA ATERRAMENTO
	CONDICIONADOR DE AR SPLIT, UNIDADE EVAPORADORA
	CONDICIONADOR DE AR CASSETE (4 VIAS) UNIDADE EVAPORADORA
	ELETROCALHA TIPO "U" PERFURADA - DIMENSÕES INFORMADAS EM PROJETO
	ELETROCALHA TIPO "U" PERFURADA - DIMENSÕES INFORMADAS EM PROJETO
	TUBULAÇÃO QUE SOBE
	TUBULAÇÃO QUE DESCE
	TUBULAÇÃO QUE PASSA
	PROJEÇÃO DE VIGA
	PROJEÇÃO DE LAJE - CAPITEI - CUBETAS
	PILAR
	ALVENARIA
	CAIXA DE PASSAGEM PVC (4x2") - HORIZONTAL E VERTICAL
	CAIXA DE PASSAGEM PVC (4x4") - HORIZONTAL E VERTICAL
	CAIXA METÁLICA LACRÁVEL (C.M.L) 50x50x20 HORIZONTAL E VERTICAL
	HASTE DE ATERRAMENTO EM COBRE

- OBS.: ANTES DE PLOTAR DAR O COMANDO REA PARA AJUSTAR AS LINHAS TRACEJADAS. NÃO PLOTAR NO MODO ECONÔMICO.
- OBSERVAR A DATA DO DESENHO NA LEGENDA DO PROJETO E DESCONSIDERAR QUALQUER VERSÃO ANTERIOR.

QUADRO DE CONTROLE DE PROJETO		
VERSÃO	DATA	DESCRIÇÃO DA MODIFICAÇÃO
V2	19/11/2024	ATUALIZAÇÃO APÓS RECEBIMENTO COM A VALIDAÇÃO / ALTERAÇÃO DA PLANTA DE PONTOS
V3	10/02/2025	VERSÃO COM ELETRODUTOS E FIÇÃO DOS APTOS TIPO
V4	21/04/2025	PROJETO ELÉTRICO COMPLETO
V5	25/04/2025	PROJETO ELÉTRICO COMPLETO COM ALTERAÇÕES SOLICITADAS PELA CONSTRUTORA
V6	21/06/2025	PROJETO ELÉTRICO COMPLETO COM ATUALIZAÇÕES DAS ÁREAS COMUNS
V7	21/07/2025	PROJETO ELÉTRICO COMPLETO COM ÚLTIMA ATUALIZAÇÃO

E EXPRESSAMENTE PROIBIDO A REPRODUÇÃO TOTAL OU PARCIAL DESTES PROJETO E TAMBÉM A SUA VEICULAÇÃO A TERCEIROS SEM A PREVIA AUTORIZAÇÃO DA EngPred - ENGENHARIA E INSTALAÇÕES PREDIAIS LTDA. DE ACORDO COM A LEI Nº 5988 ARTIGO 184 DO CÓDIGO PENAL BRASILEIRO.

Projeto	
Construtor	
Proprietário	

PROJETO: MGA MAKAI - PROJETO DE INSTALAÇÕES ELÉTRICAS

CONSTRUTOR: MGA CONSTRUÇÕES E INCORPORAÇÕES LTDA

EDIFÍCIO: MAKAI

LOCAL: AV. MAX ZAGEL, LT 05A, QD 12, LOTEAMENTO JARDIM ATLÂNTICO - CABEDELO - PB

Escala:

INDICADAS

Soluções em Eng. Energias e Sustentabilidade

Desenho:

PAV. 01: PLANTA BAIXA

QUADRO DE PROTEÇÕES

DETALHES DIVERSOS

PROJETO Nº:

23/2024

ENG. EVANDRO CESAR

CREA - 16.03.55.78.10

engpred@gmail.com

(83)3566-9776 (83)98754-9770