
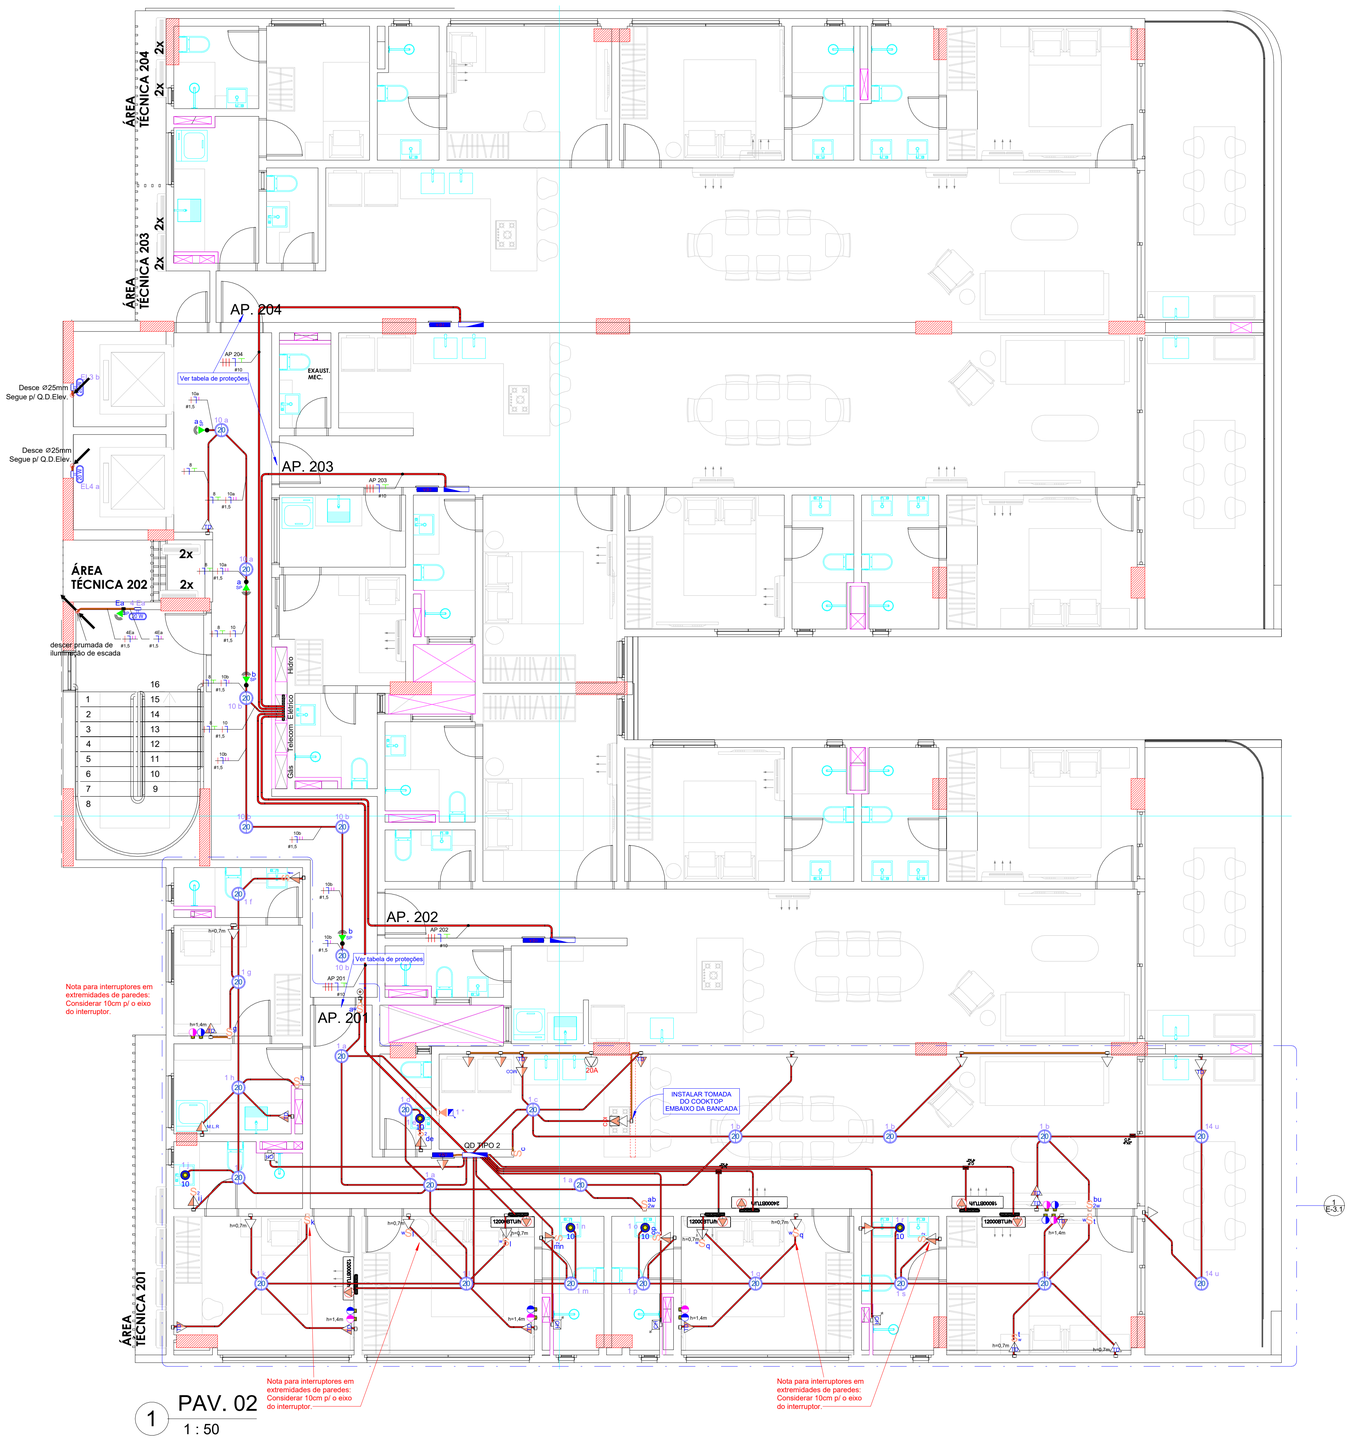


1 PAV. 02
1 : 50

DETALHE FIXAÇÃO DO ELETRODUTO

(ABRAÇADEIRA TIPO "D" DIRETA NA LAJE)

ESC._____S/E

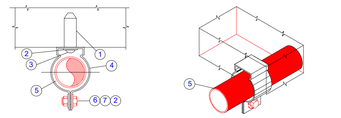


VISTA FRONTAL PERSPECTIVA

VALORES PARA UM MÓDULO DE FIXAÇÃO			
ITEM	D E S C R I Ç Ã O	UNID	QUANT.
01	BUCHA DE EXPANSÃO - NYLON - ∅ 10mm	PÇ	1
02	ARRUELA LISA ∅ 5/16"	PÇ	2
03	PARAFUSO ROSCA LIGEIRA, FENDA PHILIPS, 40x6mm	PÇ	1
04	ABRAÇADEIRA "D" (1/2" - 3/4" - 1")	PÇ	1
05	ELETRODUTO ∅ 1/2", 3/4", 1"	m	Variável
06	PARAFUSO C/ CABEÇA SEXTAVADA ∅ 1/4" x 3/4"	PÇ	1
07	PORCA SEXTAVADA ∅1/4"	PÇ	1

DET. DE ENCAMISAMENTO

(P/ PASSAGEM DE ELETRODUTO EM VIGA)


ESC_____S/E

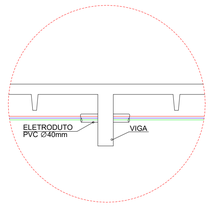


ELETRODUTO EMBUTIDO EM VIGA

(VISTA EM CORTE)

ESCALA _____S/E

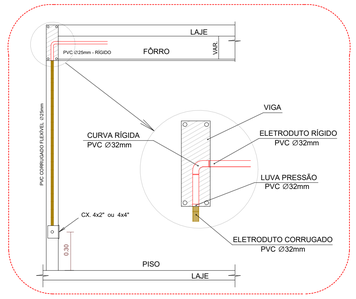

DESVIO DE ELETRODUTOS DA ESTRUTURA

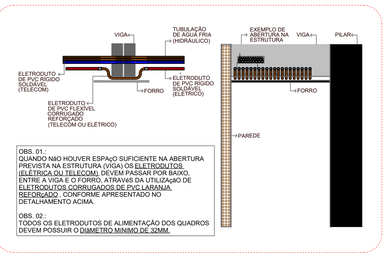

OBS. 01 :-
QUANDO NAO HOUVER ESPAçO SUFICIENTE NA ABERTURA PREVISTA NA ESTRUTURA (VIGA) OS ELETRODUTOS (ELÉTRICA OU TELECOM) DEVEM PASSAR POR BAIXO, ENTRE A VIGA E O FORRO, ATRAVÉS DA UTILIZAçãO DE ELETRODUTOS CORRUGADOS DE PVC LARANJA REFORçADO , CONFORME APRESENTADO NO DETALHAMENTO ACIMA.

OBS. 02
TODOS OS ELETRODUTOS DE ALIMENTAÇÃO DOS QUADROS DEVEM POSSUIR O DIAMETRO MINIMO DE 32MM.

MGA MAKAI - QUADRO DE PROTEÇÕES

NÚMERO DAS UNIDADES	TIPO DE LAYOUT	TIPO DE QUADRO
001	TIPO A	TIPO 1
101	TIPO B (COM VARANDA EM L)	TIPO 2
201, 301, 401, 501, 601, 701	TIPO B	TIPO 2
102, 202, 302, 402, 502, 602, 702	TIPO C	TIPO 3
103, 203, 303, 403, 503, 603, 703	TIPO D	
104, 204, 304, 404, 504, 604, 704	TIPO E	
801	TIPO F	TIPO 4

LEGENDA

	RODA-TETO A SER EXECUTADO PARA VIABILIZAR AS INSTALAçõES
	ENGROSSO A SER EXECUTADO PARA VIABILIZAR AS INSTALAçõES
	PONTO PARA CHUVEIRO 32A, H=2.20M. UTILIZAR CONECTOR DE EMENDA TIPO BARRA 06 BORNES (VERTICAL E HORIZONTAL)
	EXAUSTOR MECÂNICO
	CAIXA 4x4" TIPO CONDULETE COM TAMPA CEGA
	CAIXA 4x4" TIPO PVC COM TAMPA CEGA
CAR #1 ou #3	CARREGADOR VEICULAR INDIVIDUAL - H=1,5m (Mono ou Tifásico)
CAR #1 ou #3	CARREGADOR VEICULAR COLETIVO- H=1,5m (Mono ou Tifásico)
	TOMADA PARA AR-CONDICIONADO H=2.50m
USB USB	PONTO DE TOMADA, SIMPLES E DUPLO, 10A + 1 MÓDULO USB
	PONTO DE TOMADA, 20A - (VERTICAL E HORIZONTAL) - VERIFICAR AS ALTURAS ABAIXO
	TOMADA ALTA H=2.20m, 10A - (VERTICAL E HORIZONTAL)
	TOMADA MÉDIA H=1.20m, 10A - (VERTICAL E HORIZONTAL) - MODO GERAL TOMADA MEDIA. H=1.50m, 10A - (VERTICAL E HORIZONTAL) - PONTO PARA TV
	TOMADA BAIXA H=0.30m, 10A - (VERTICAL E HORIZONTAL)
	TOMADA TRIPLA, 10A - (VERTICAL E HORIZONTAL)
	TOMADA DUPLA, 10A - (VERTICAL E HORIZONTAL)
	PONTO DE FORÇA PARA MOTOR DE PORTÃO DE GARAGEM - 1/2 CV
	TOMADA DE TETO - EMBUTIDA NO FORRO OU LAJE, 10A (SIMPLES E DUPLA)
	TOMADA DE TETO - EMBUTIDA NO FORRO OU LAJE, 20A (SIMPLES E DUPLA)
	TOMADA DE PISO SIMPLES E DUPLA, 10A
	TOMADA DE PISO SIMPLES E DUPLA, 20A
COS	TOMADA ALTA COIFA FOGÃO H=1.80m, 10A
MICO MICO	TOMADA P/ FORNO MICROONDAS (F/N/T) 20A, H=1.60m (VERTICAL E HORIZONTAL)
FRN	TOMADA P/ FORNO ELÉTRICO (F/N/T) 20A, H=0.60m
COK1X COK1X	TOMADA P/ COOKTOP (F/N/T) 20A, H=0.60m - COOKTOP 2 E 4 BOCAS
MLR	TOMADA MÁQUINA LAVAR ROUPA (F/N/T) 20A, H=1.20m
	PONTO PARA INTERFONE H=1.40m
	PONTO BAIXO PARA ANTENA COLETIVA H=0.30m
	PONTO MÉDIO PARA ANTENA COLETIVA H=1.50m
	PONTO ALTO PARA ANTENA COLETIVA H=1.80m
	TOMADA MÉDIA PARA TELEFONE H=1.20m
	TOMADA BAIXA PARA TELEFONE H=0.30m
	PONTO BAIXO PARA TV ASSINATURA H=0.30m
	PONTO MÉDIO PARA TV ASSINATURA H=1.50m
	PONTO ALTO PARA TV ASSINATURA H=1.80m
n	INTERRUPTOR DE "n" SEÇÕES, H=1,20m
S	INTERRUPTOR SIMPLES 10A, H=1,20m
Sw	INTERRUPTOR PARALELO, H=1,20m
SFw	INTERRUPTOR INTERMEDIÁRIO, H=1,20m
	BOTOEIRA PARA CAMPAINHA ,H=1,20m
	PONTO PARA CAMPAINHA H=2.10m
(W)	LUMINÁRIA PLAFON CIRCULAR DE SOBREPOR P/ CIRCUITO DE ILUMINAÇÃO VIGA
(W)	LUMINÁRIA PLAFON CIRCULAR DE SOBREPOR NO FORRO
(W)	LUMINÁRIA PLAFON QUADRADA DE SOBREPOR NO FORRO
(W)	SPOT LED QUADRADO EMBUTIDO NO FORRO
(W)	SPOT LED REDONDO EMBUTIDO NO FORRO
(W)	SPOT LED REDONDO (DUPLO) EMBUTIDO NO FORRO
	LUMINÁRIA FLUORESCENTE NA PAREDE 20W, H=1,8m
20 W	PONTO DE REFLETOR NA PAREDE 20W, H=2,20m OU INDICADO
20 W	PONTO DE ILUMINAÇÃO DE PAREDE - ARANDELA 20W, H=1,5m OU INDICADO
TRILHO	TRILHO ELETRIFICADO - 10W POR SPOT
	LUMINÁRIA TIPO REFLETOR LED - 50W P/ FIXAÇÃO EM POSTE METÁLICO
(W)	BALIZADOR DE PISO
	FITA DE LED NO TETO E PAREDE - (VER POTÊNCIA EM PLANTA BAIXA)
	FITA DE LED NO PISO - (VER POTÊNCIA EM PLANTA BAIXA)
DRIVER	CAIXA OCTOGONAL OU 4x2" + FONTE (DRIVER) PARA FITA DE LED
9W Ilum. Sub.	CAIXA SODRAMAR, PARA UTILIZAÇÃO NA ILUMINAÇÃO DA PISCINA.
SP	SENSORES DE PRESENÇA DE TETO
SP	SENSOR DE PRESENÇA DE PAREDE
	CONDUTORES NEUTRO, FASE, TERRA E RETORNO
	ELETRODUTO PVC RIGIDO NO ENTREFORRO OU EMBUTIDO NA LAJE
	ELETRODUTO PVC CORRUGADO REFORÇADO EMBUTIDO NA PAREDE
	ELETRODUTO PVC RIGIDO SOB LAJE DE PISO
	ELETRODUTO PVC RÍGIDO NO PISO PARA ATERRAMENTO
	CONDICIONADOR DE AR SPLIT, UNIDADE EVAPORADORA
	CONDICIONADOR DE AR CASSETE (4 VIAS) UNIDADE EVAPORADORA
	ELETROCALHA TIPO "U" PERFURADA - DIMENSÕES INFORMADAS EM PROJETO
	ELETROCALHA TIPO "U" PERFURADA - DIMENSÕES INFORMADAS EM PROJETO
	TUBULAÇÃO QUE SOBE
	TUBULAÇÃO QUE DESCE
	TUBULAÇÃO QUE PASSA
	PROJEÇÃO DE VIGA
	PROJEÇÃO DE LAJE - CAPITEL - CUBETAS
	PILAR
	ALVENARIA
	CAIXA DE PASSAGEM PVC (4x2") - HORIZONTAL E VERTICAL
	CAIXA DE PASSAGEM PVC (4x4") - HORIZONTAL E VERTICAL
	CAIXA METÁLICA LACRÁVEL (C.M.L.) 50x50x20 HORIZONTAL E VERTICAL
	HASTE DE ATERRAMENTO EM COBRE

- OBS.: ANTES DE PLOTAR DAR O COMANDO REA PARA AJUSTAR AS LINHAS TRACEJADAS.
NÃO PLOTAR NO MODO ECONÔMICO.

- OBSERVAR A DATA DO DESENHO NA LEGENDA DO PROJETO E DESCONSIDERAR QUALQUER VERSÃO ANTERIOR.

QUADRO DE CONTROLE DE PROJETO

VERSÃO	DATA	DESCRIÇÃO DA MODIFICAÇÃO
V2	19/11/2024	ATUALIZAÇÃO APÓS RECEBIMENTO COM A VALIDAÇÃO / ALTERAÇÃO DA PLANTA DE PONTOS
V3	10/02/2025	VERSÃO COM ELETRODUTOS E FIAÇÃO DOS APTOS TIPO
V4	21/04/2025	PROJETO ELÉTRICO COMPLETO
V5	25/04/2025	PROJETO ELÉTRICO COMPLETO COM ALTERAÇÕES SOLICITADAS PELA CONSTRUTORA
V6	21/06/2025	PROJETO ELÉTRICO COMPLETO COM ATUALIZAÇÕES DAS ÁREAS COMUNS
V7	21/07/2025	PROJETO ELÉTRICO COMPLETO COM ÚLTIMA ATUALIZAÇÃO

É EXPRESSAMENTE PROIBIDO A REPRODUÇÃO TOTAL OU PARCIAL DESTE PROJETO E TAMBÉM A SUA VEICULAÇÃO A TERCEIROS SEM A PRÉVIA AUTORIZAÇÃO DA EngPred - ENGENHARIA E INSTALAÇÕES PREDIAIS LTDA, DE ACORDO COM A LEI Nº 5988 ARTIGO 184 DO CÓDIGO PENAL BRASILEIRO.

Projeto

Construtor

Proprietário

PROJETO: MGA MAKAI - PROJETO DE INSTALAÇÕES ELÉTRICAS
CONSTRUTOR: MGA CONSTRUÇÕES E INCORPORAÇÕES LTDA
EDIFÍCIO: MAKAI
LOCAL: AV. MAX ZAGEL, LT 05A, QD 12, LOTEAMENTO JARDIM ATLÂNTICO - CABEDELO - PB

E-4.0

Escala: INDICADAS

TecPred
Soluções em Eng., Energias e Sustentabilidade
ENG. EVANDRO CESAR
CREA - 16.03.55.76.10
engpred@gmail.com
(83)3566-0770 (83)98755-0770

Desenho : PAV. 02 AO 07: PLANTA BAIXA
QUADRO DE PROTEÇÕES
DETALHES DIVERSOS

PROJETO Nº: 23/2024

DATA: 21/07/2025

PROJETADO POR: ENGª
GIORDANNA PERRUSI MONTENEGRO LEAL