


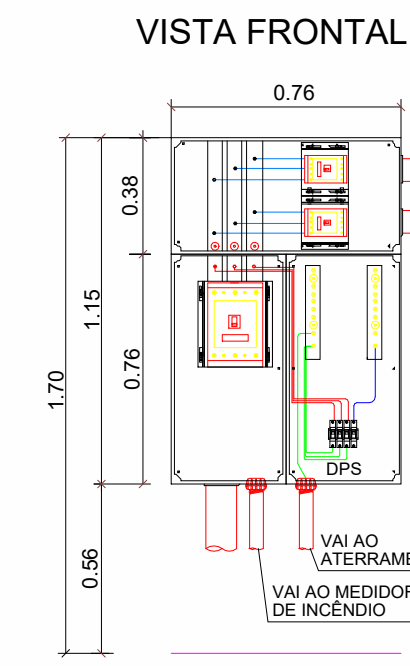
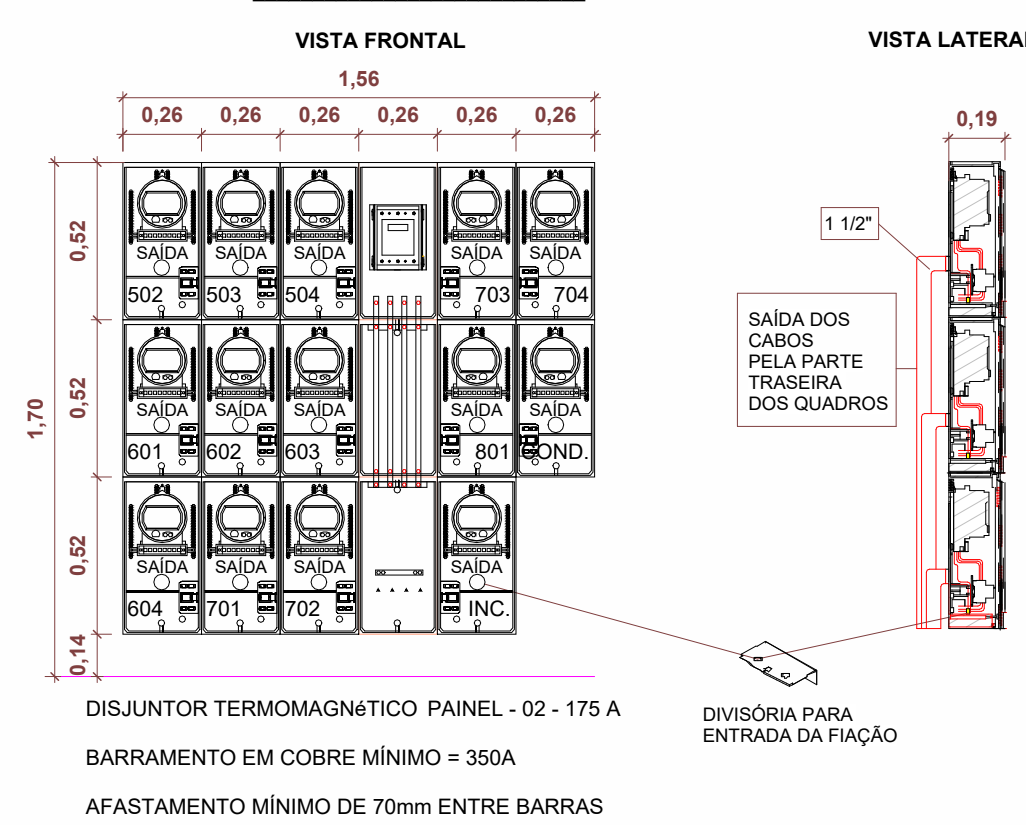
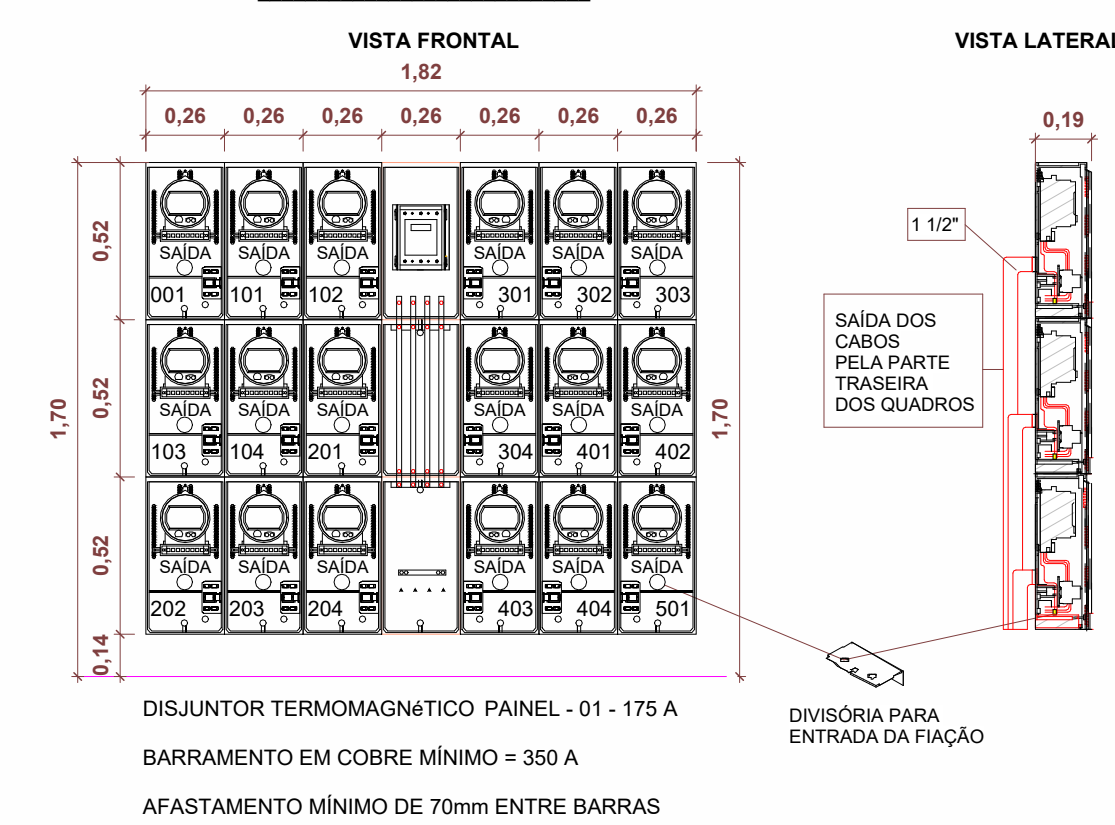
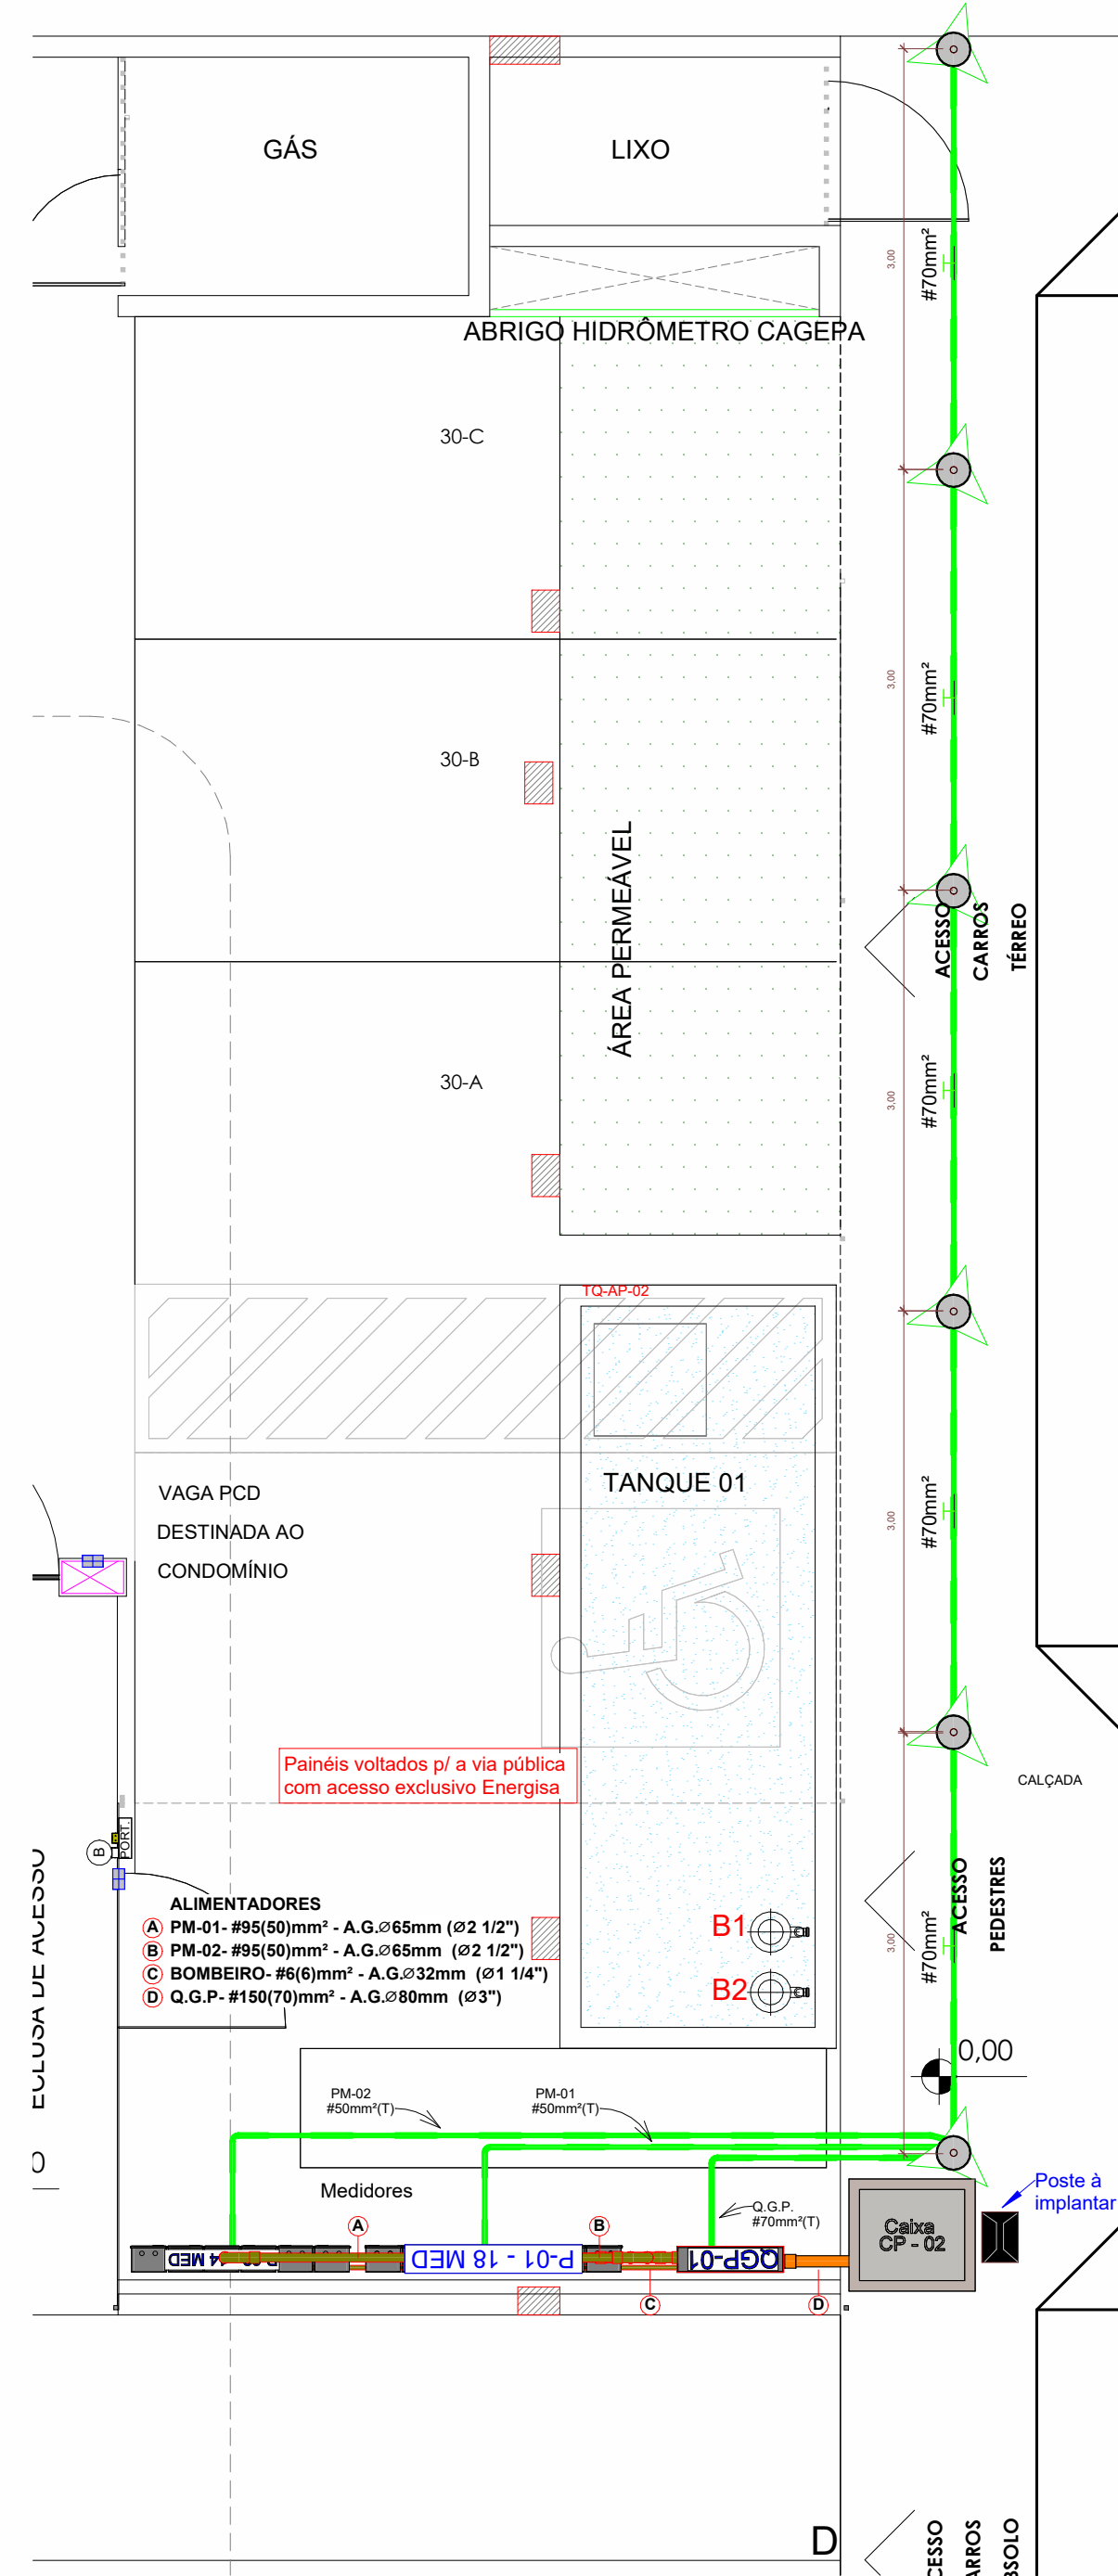
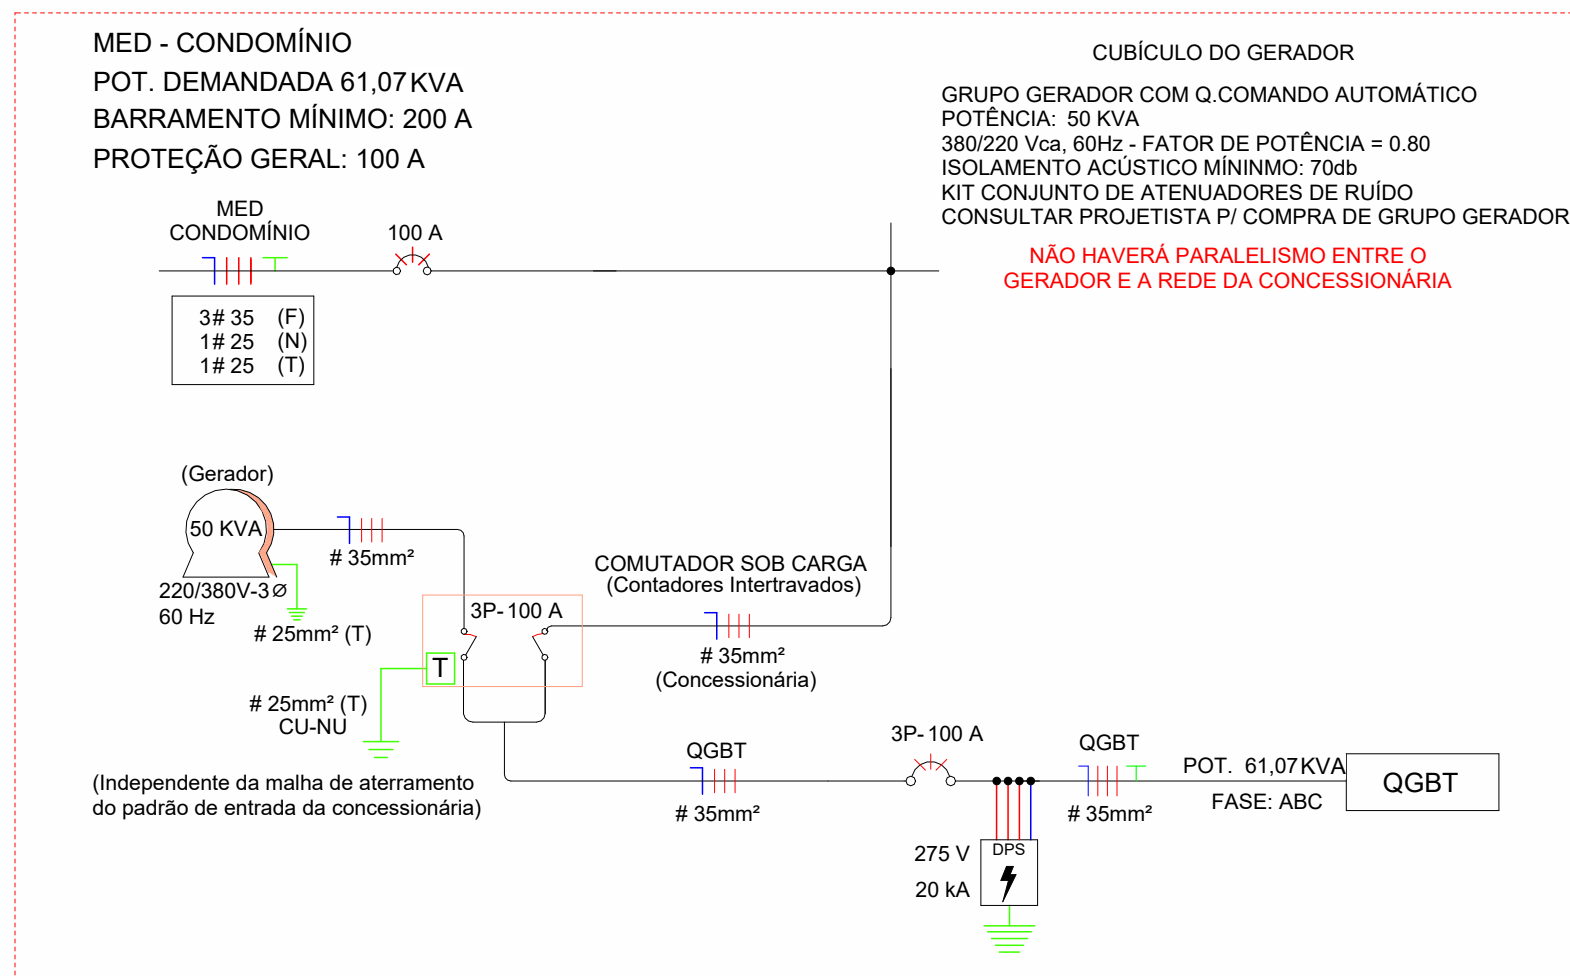
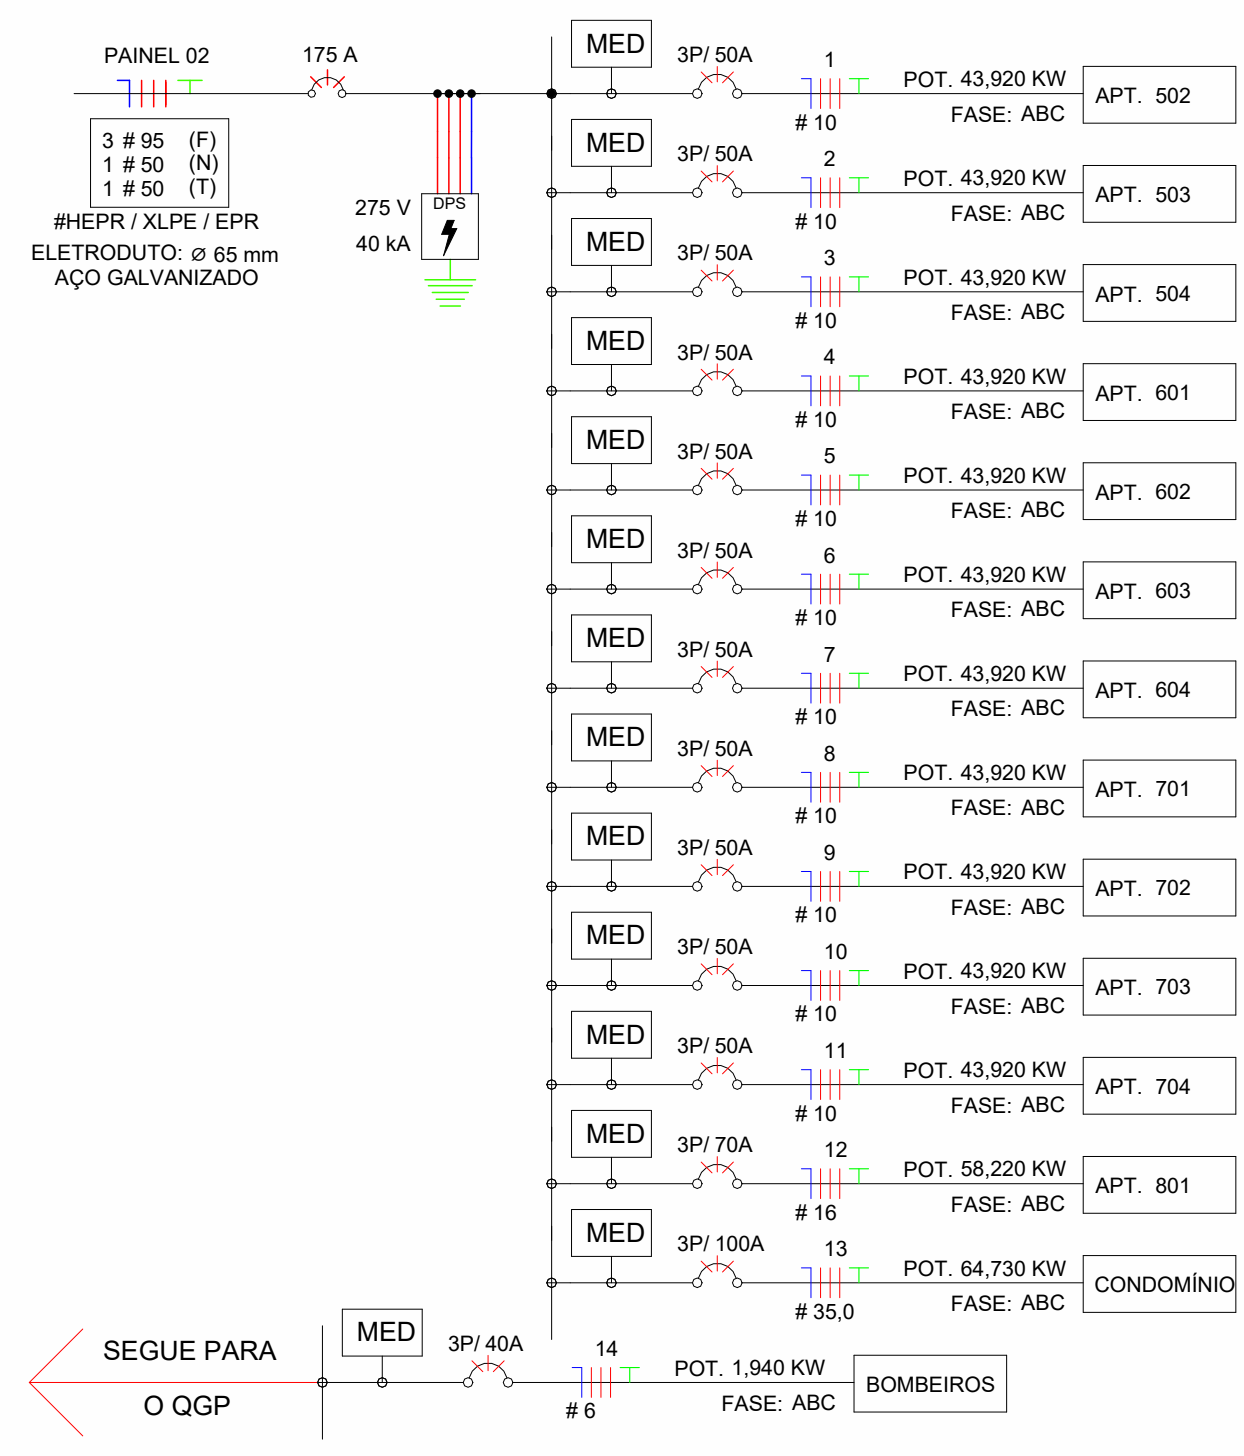


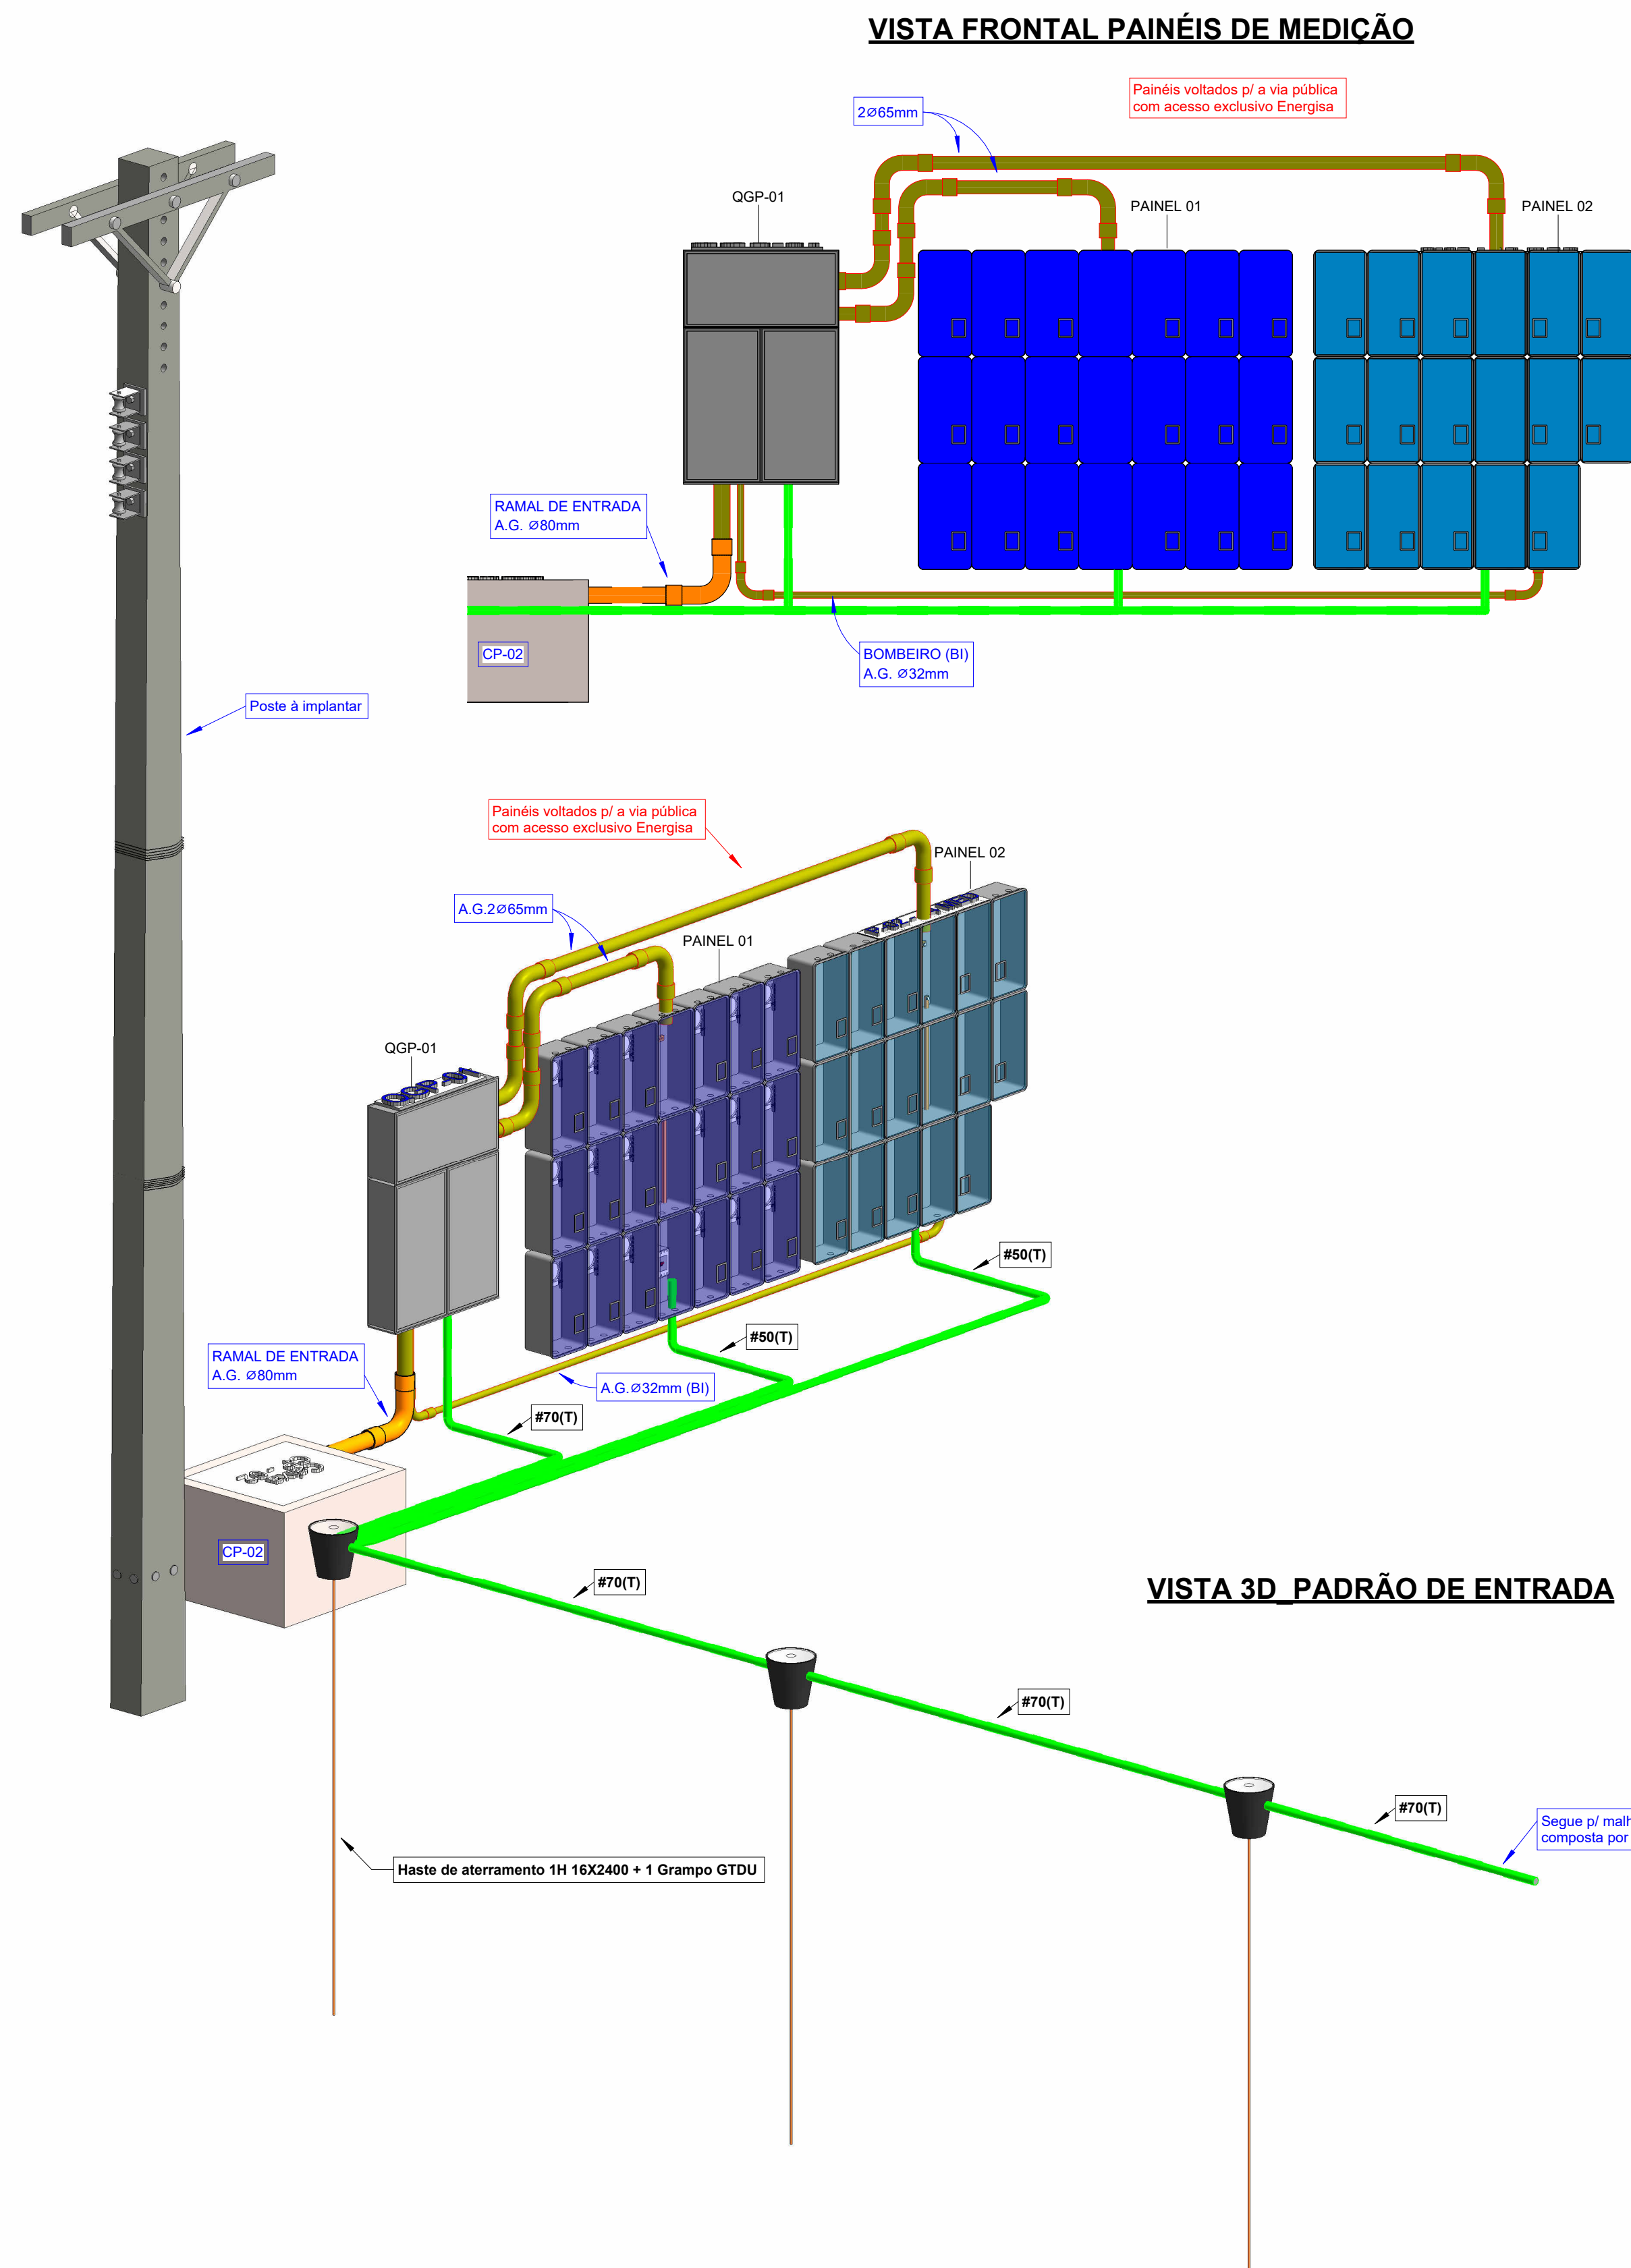

		Q.G.P. - 220 V		ARPANDO EM COBRE SEÇÃO TRANSVERSAL		QGP-01	
		Q.G.P. - 1" x 5/16"					
DESCRIÇÃO	DEMANDA (KVA)	3Ø V	T	175	175	FASE DO CIRCUITO	OBSERVAÇÕES
PANEL 01	82,02 KVA	3Ø V	T	175	#150(S)	A - B - C	CALCULADO PELA DEMANDA
PANEL 02	108,40 KVA	3Ø V	T	175	#150(S)	A - B - C	CALCULADO PELA DEMANDA
TOTAL	138,97 KVA	3Ø V	T	225,00	#150(70)	A-B-C	CALCULADO PELA DEMANDA




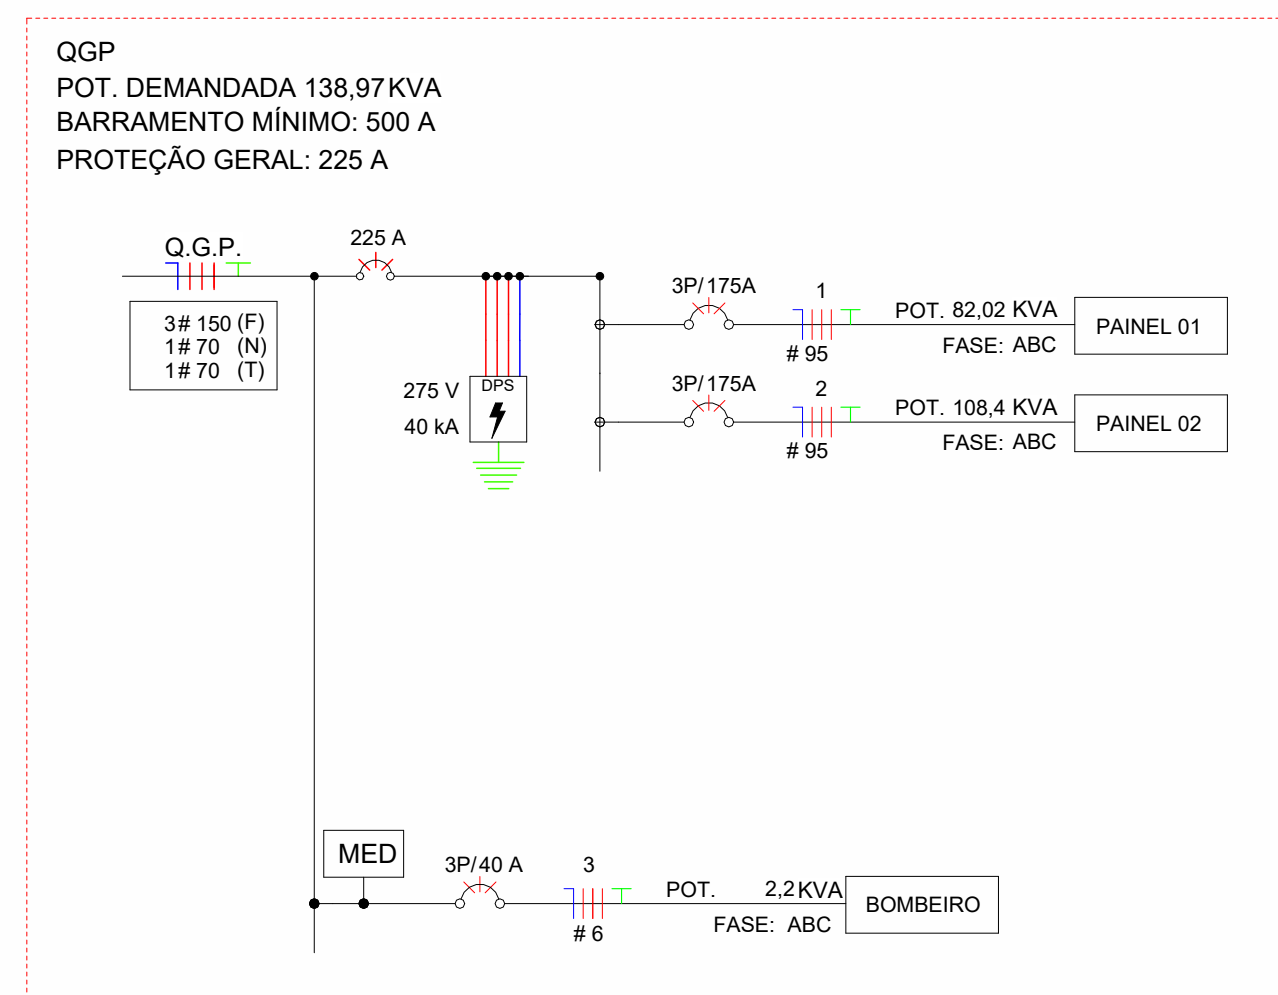


TÉRREO - ALIMENTADORES

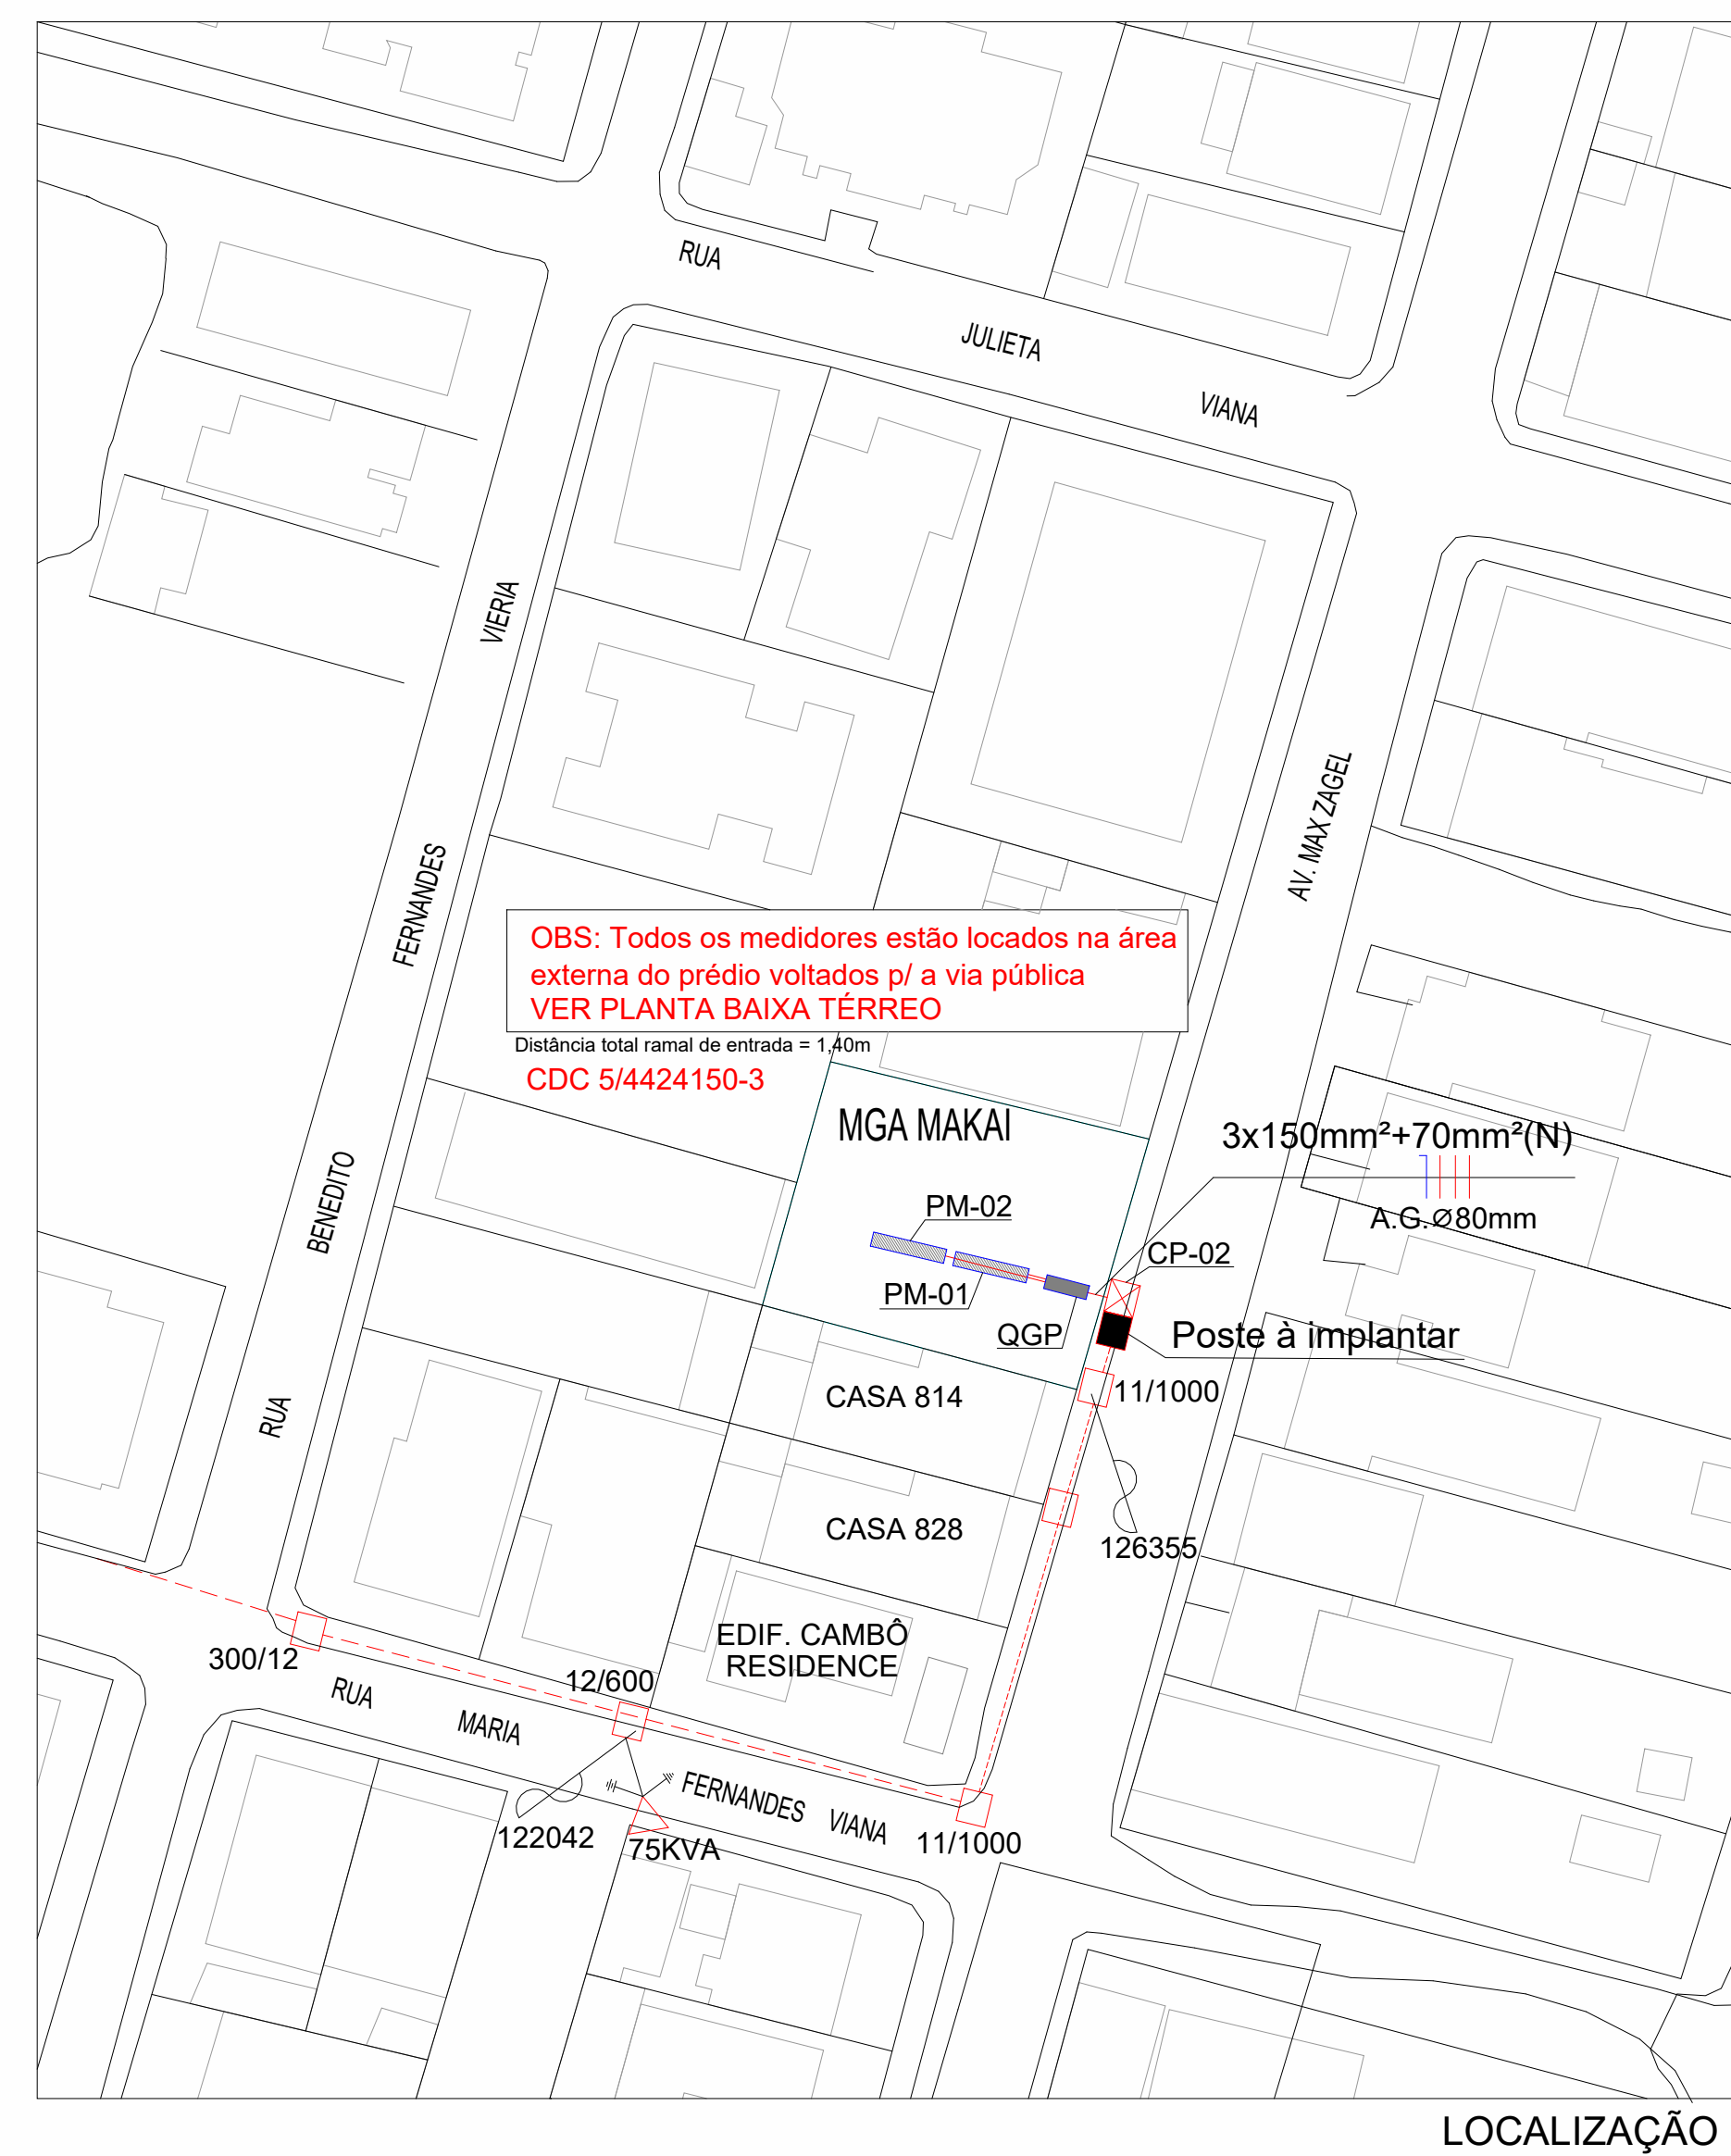

SIMBOLOGIA	
	REDE DE BAIXA
	REDE DE ALTA
	POSTE EXISTENTE
	POSTE À INSTALAR
	POSTE À RETIRAR
	CHAVE SECCIONADORA EXISTENTE
	CHAVE SECCIONADORA À INSTALAR
	CHAVE SECCIONADORA À RETIRAR
	TRANSFORMADOR EXISTENTE
	TRANSFORMADOR À INSTALAR
	TRANSFORMADOR À RETIRAR
	MEDIDOR
	CAIXA METÁLICA LACRÁVEL (C.M.L.)

- 1- Os condutores para a ramais de entrada, deverão possuir isolamento do tipo XLPE ou HEPR 90°C para 0,6/1kV
- 2- Os condutores para os ramos subterâneos, deverão possuir isolamento do tipo XLPE ou HEPR 90°C para 0,6/1kV e os outros tipos de cabos.
- 3- A caixa de medição deverá conter marcação dos números de aptos ou lotes.
- 4- Para bitolas acima de 6mm² é obrigatório o uso de cabos.
- 5- Instalar no poste placa de identificação do eletroduto do ramal de entrada, contendo o número e o número atual do prédio.
- 6- Utilizar cabos de 1/2" curva 130° no eletroduto do ramal de entrada.
- 7- As barras deverão ser instaladas com um afastamento mínimo de 70mm, entre si e com relação à outras partes metálicas (exceto nos pontos de fixação por isoladores).
- 8- Fixar o eletroduto do ramal de entrada ϕ 1,9 19mm + varo roscado ϕ 1/4" à abasagrada tipo ômega.
- 9- As armadilhas estão em milímetros.
- 10- As larguras mostradas são valores mínimos.
- 11- O barramento de terra não deve ser isolado do centro de medição.
- 12- Todos os condutores terra, das instalações deverão ser conectados ao barramento terra.
- 13- Todos os condutores terra dos quadros e caixas deverão ser conectados ao barramento terra.
- 14- O cubículo de medição ou o ambiente desta deverá ser fumado artificialmente.
- 15- Os condutores das medições trifásicas, deverão possuir isolamento do tipo XLPE ou HEPR 90°C para 0,6/1kV
- 16- Os condutores das medições monofásicas, deverão possuir isolamento do tipo XLPE ou HEPR 90°C para 0,6/1kV
- 17- Eletroduto ramal de entrada subida lateral do poste. Ao galvanizado a fogo tipo pesado
- 18- Eletroduto instalado após CP-01 ou CP-02: PVC roscaável
- 19- Eletrodutos PVC àço galvanizado devem ser roscaáveis (NBR-15465)
- 20- Nas caixas de passagem CP-01 ou CP-02 deixar sobra de cabo de no mínimo 2 metros
- 21- As partes metálicas não energizadas serão estanques.
- 22- O pedido de vistoria e ligação deverá ser feito pelo CONTRATANTE ou CONTRATADO do ART de ENLACE/LO com INTENÇÃO DE FIM (NOVENA) DIAS da data de entrega do empreendimento, prazo necessário para elaboração de projeto e execução de obra de rede e de reforma ou conservação de distribuição.
- 23- DPS: 490kV - Poleitar contra surto ruidoso, rede baixa tensão, tensão operação: 220/380V; corrente descarga: 40kA; grau proteção: IP 20; proteção sistema: sim, impulso suportado: superior 2,5kA; referência: NCU 010, NBR 5410, NBR 5411, NBR 5412,NBR 58

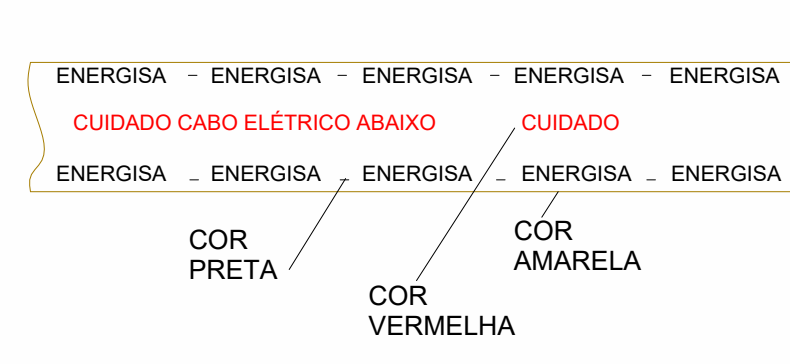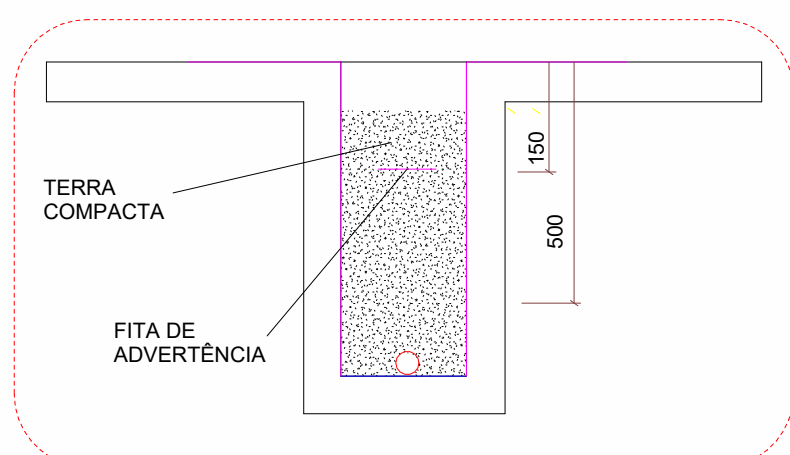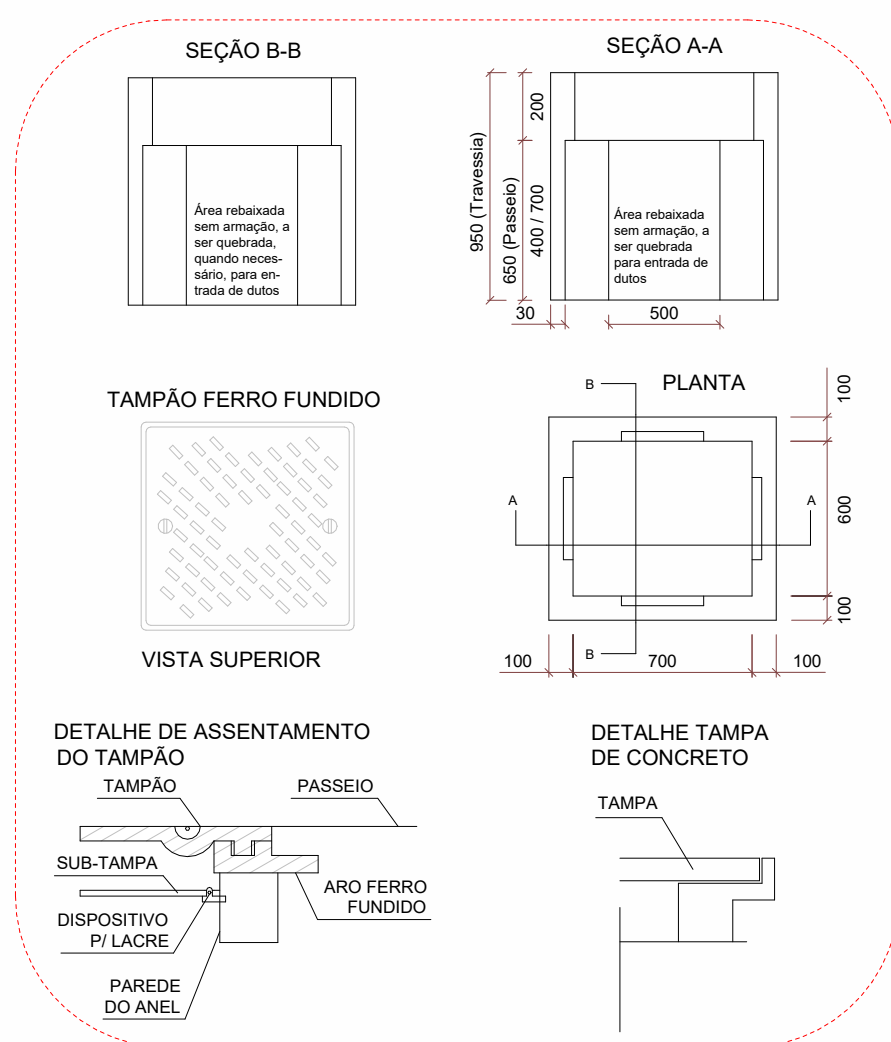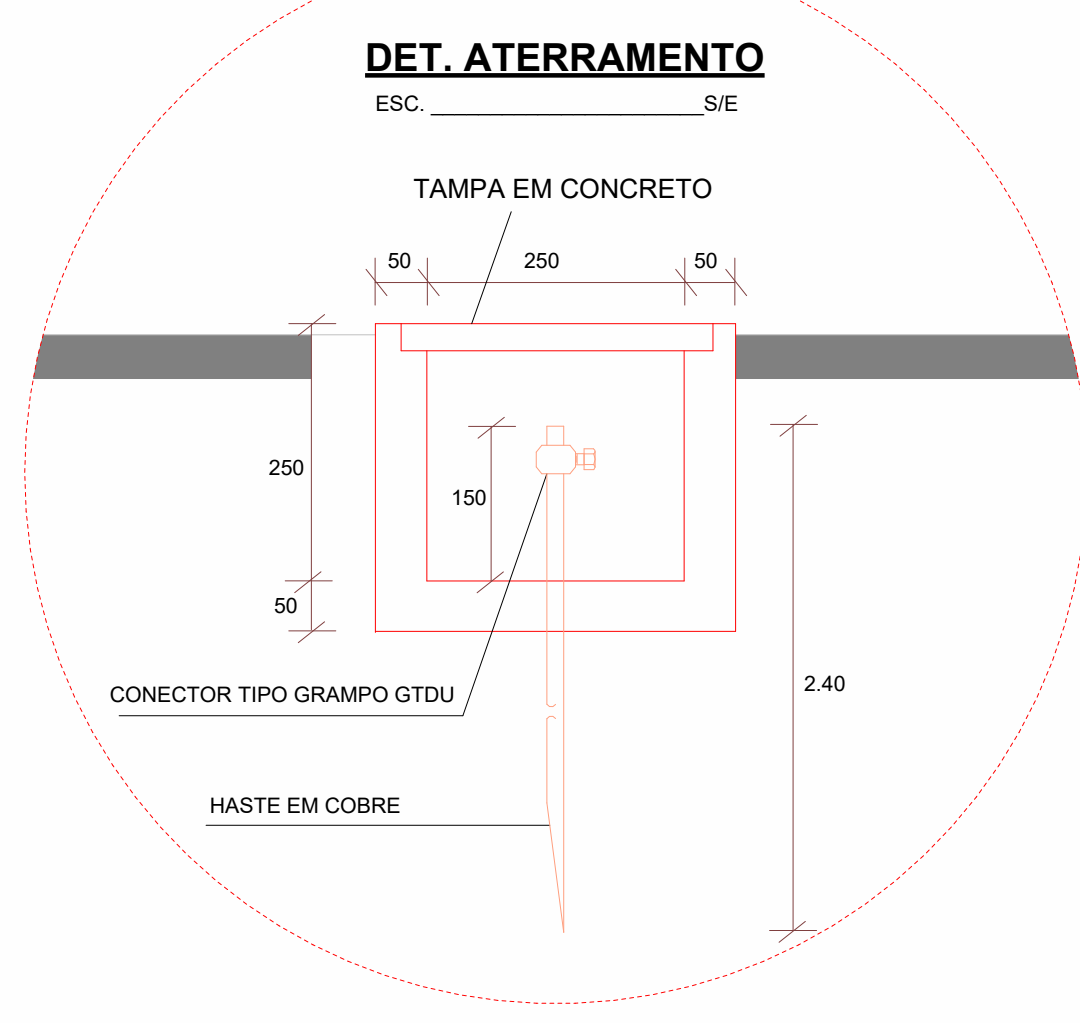

- OBS.: ANTES DE PLOTAR DAR O COMANDO REA PARA AJUSTAR AS LINHAS TRACEJADAS. NÃO PLOTAR NO MODO ECONÔMICO.
- OBSERVAR A DATA DO DESENHO NA LEGENDA DO PROJETO E DESCONSIDERAR QUALQUER VERSÃO ANTERIOR

[illegible]

É EXPRESSAMENTE PROIBIDO A REPRODUÇÃO TOTAL OU PARCIAL DESTE PROJETO E TAMBÉM A SUA VEICULAÇÃO A TERCEIROS SEM A PRÉVIA AUTORIZAÇÃO DA EngPred - ENGENHARIA E INSTALAÇÕES PREDIAIS LTDA, DE ACORDO COM A LEI Nº 5988 ARTIGO 184 DO CÓDIGO PENAL BRASILEIRO.

Projeto _____

Construtor _____

Proprietário _____

PROJETO: MGA MAKAI - PROJETO DE INSTALAÇÕES ELÉTRICAS
CONSTRUTOR: MGA CONSTRUÇÕES E INCORPORAÇÕES LTDA
EDIFÍCIO: MAKAI

LOCAL: AV. MAX ZAGEL, LT 05A, QD 12, LOTEAMENTO JARDIM ATLÂNTICO - CABEDELO - PB

Escala:

INDICADAS

 **TecPred**
Soluções em Eng., Energias e Sustentabilidade



ENG. EVANDRO CESAR
CREA - 16.03.55.76.10
engpred@gmail.com
(83)3566-0770 (83)98755-07

DATA: 21/07/2025	Desenho : PAINÉIS DE ENTRADA E MEDIÇÃO LOCALIZAÇÃO DETALHES DIVERSOS	PROJETO Nº: 23/2024
------------------	--	-------------------------------

PROJETADO POR: